

REPUBLIK INDONESIA  
KEMENTERIAN HUKUM DAN HAK ASASI MANUSIA

# SURAT PENCATATAN CIPTAAN

Dalam rangka perlindungan ciptaan di bidang ilmu pengetahuan, seni dan sastra berdasarkan Undang-Undang Nomor 28 Tahun 2014 tentang Hak Cipta, dengan ini menerangkan:

Nomor dan tanggal permohonan : EC00202469113, 20 Juli 2024

## Pencipta

Nama : **Ir. Irina Mildawani, MT., PhD., Dr. Rehulina Apriyanti, ST., MT. dkk**

Alamat : Bukit Pamulang Indah Blok. E22 No 10. RT/RW 002/005, Kelurahan Pamulang Timur, Pamulang, Tangerang Selatan, Banten, 15417

Kewarganegaraan : Indonesia

## Pemegang Hak Cipta

Nama : **Universitas Gunadarma**

Alamat : Jl Margonda Raya No. 100 Pondok Cina, Beji, Depok, Jawa Barat 16424

Kewarganegaraan : Indonesia

Jenis Ciptaan : **Arsitektur**

Judul Ciptaan : **Desain Pintu Gerbang Pesantren Ulul Ilmi, Jakarta Timur**

Tanggal dan tempat diumumkan untuk pertama kali di wilayah Indonesia atau di luar wilayah Indonesia : 20 Juli 2024, di Depok

Jangka waktu perlindungan : Berlaku selama 50 (lima puluh) tahun sejak Ciptaan tersebut pertama kali dilakukan Pengumuman.

Nomor pencatatan : 000644464

adalah benar berdasarkan keterangan yang diberikan oleh Pemohon.

Surat Pencatatan Hak Cipta atau produk Hak terkait ini sesuai dengan Pasal 72 Undang-Undang Nomor 28 Tahun 2014 tentang Hak Cipta.



a.n. MENTERI HUKUM DAN HAK ASASI MANUSIA  
DIREKTUR JENDERAL KEKAYAAN INTELEKTUAL  
u.b

Direktur Hak Cipta dan Desain Industri

IGNATIUS M.T. SILALAH  
NIP. 196812301996031001

## Disclaimer:

Dalam hal pemohon memberikan keterangan tidak sesuai dengan surat pernyataan, Menteri berwenang untuk mencabut surat pencatatan permohonan.

**LAMPIRAN PENCIPTA**

| No | Nama                                    | Alamat   |
|----|-----------------------------------------|---|
| 1  | Ir. Irina Mildawani, MT., PhD.          | Bukit Pamulang Indah Blok. E22 No 10. RT/RW 002/005, Kelurahan Pamulang Timur, Pamulang, Tangerang Selatan |
| 2  | Dr. Rehulina Apriyanti, ST., MT.        | Kp. Pedurenan RT/RW 005/007, Kelurahan Harjamukti, Cimanggis, Depok                                        |
| 3  | Dr. Veronika Widi Prabawasari, ST., MT. | Bella Casa Residence Blok A1-11 RT/RW 003/005 Kelurahan Depok , Pancoran Mas, Depok                        |
| 4  | Purwanto Joko Slameto, S.T., M.T.       | Jl. Baru Dipo KRL No.150, Ratu Jaya RT/RW 003/003, Kelurahan Ratu Jaya , Cipayung, Depok                   |
| 5  | Bima Haryadi, S.T., M.Ars.              | Jl. Masjid RT008/07 No.84, Susukan, Ciracas, Jakarta Timur, DKI Jakarta, Ciracas, Jakarta Timur            |
| 6  | Remigius Hari Susanto, ST., MT          | Jl. Raden Saleh IV No.C37 RT/RW 04/05, Kelurahan Sukmajaya, Sukmajaya, Depok                               |
| 7  | Agus Nugroho, ST., MT                   | Kp. Pitara No. 52 Rt 002/006, Rangkapan Jaya, Pancoran Mas, Depok                                          |
| 8  | Dr. Dimyati, ST., MT                    | Kp. Pitara RT/RW 002/006, Kelurahan Rangkapan Jaya , Pancoran Mas, Depok                                   |
| 9  | Dr. Sulardi, ST., MT                    | Palsigunung, No 82 RT 02/RW 02 , Kelurahan Mekarsari, Cimanggis, Depok                                     |
| 10 | Dr. Paranita Asnur, S.Hut., M.Si        | Kencana Residence RT 03 RW 14 KA 9 No 14, Kelurahan Kencana, Tanah Sereal, Bogor                           |
| 11 | Kiemas Hanipurbaya                      | Komp. Taman Firdaus Blok B No.12 RT/RW 004/010, Kelurahan Situgede, Bogor Barat - Kota, Bogor              |






# DESAIN PINTU GERBANG —


PESANTREN ULUL ILMI, JAKARTA TIMUR



URBAN FARMING  
PONDOK PESANTREN ULUL ILMI HYDROFARM

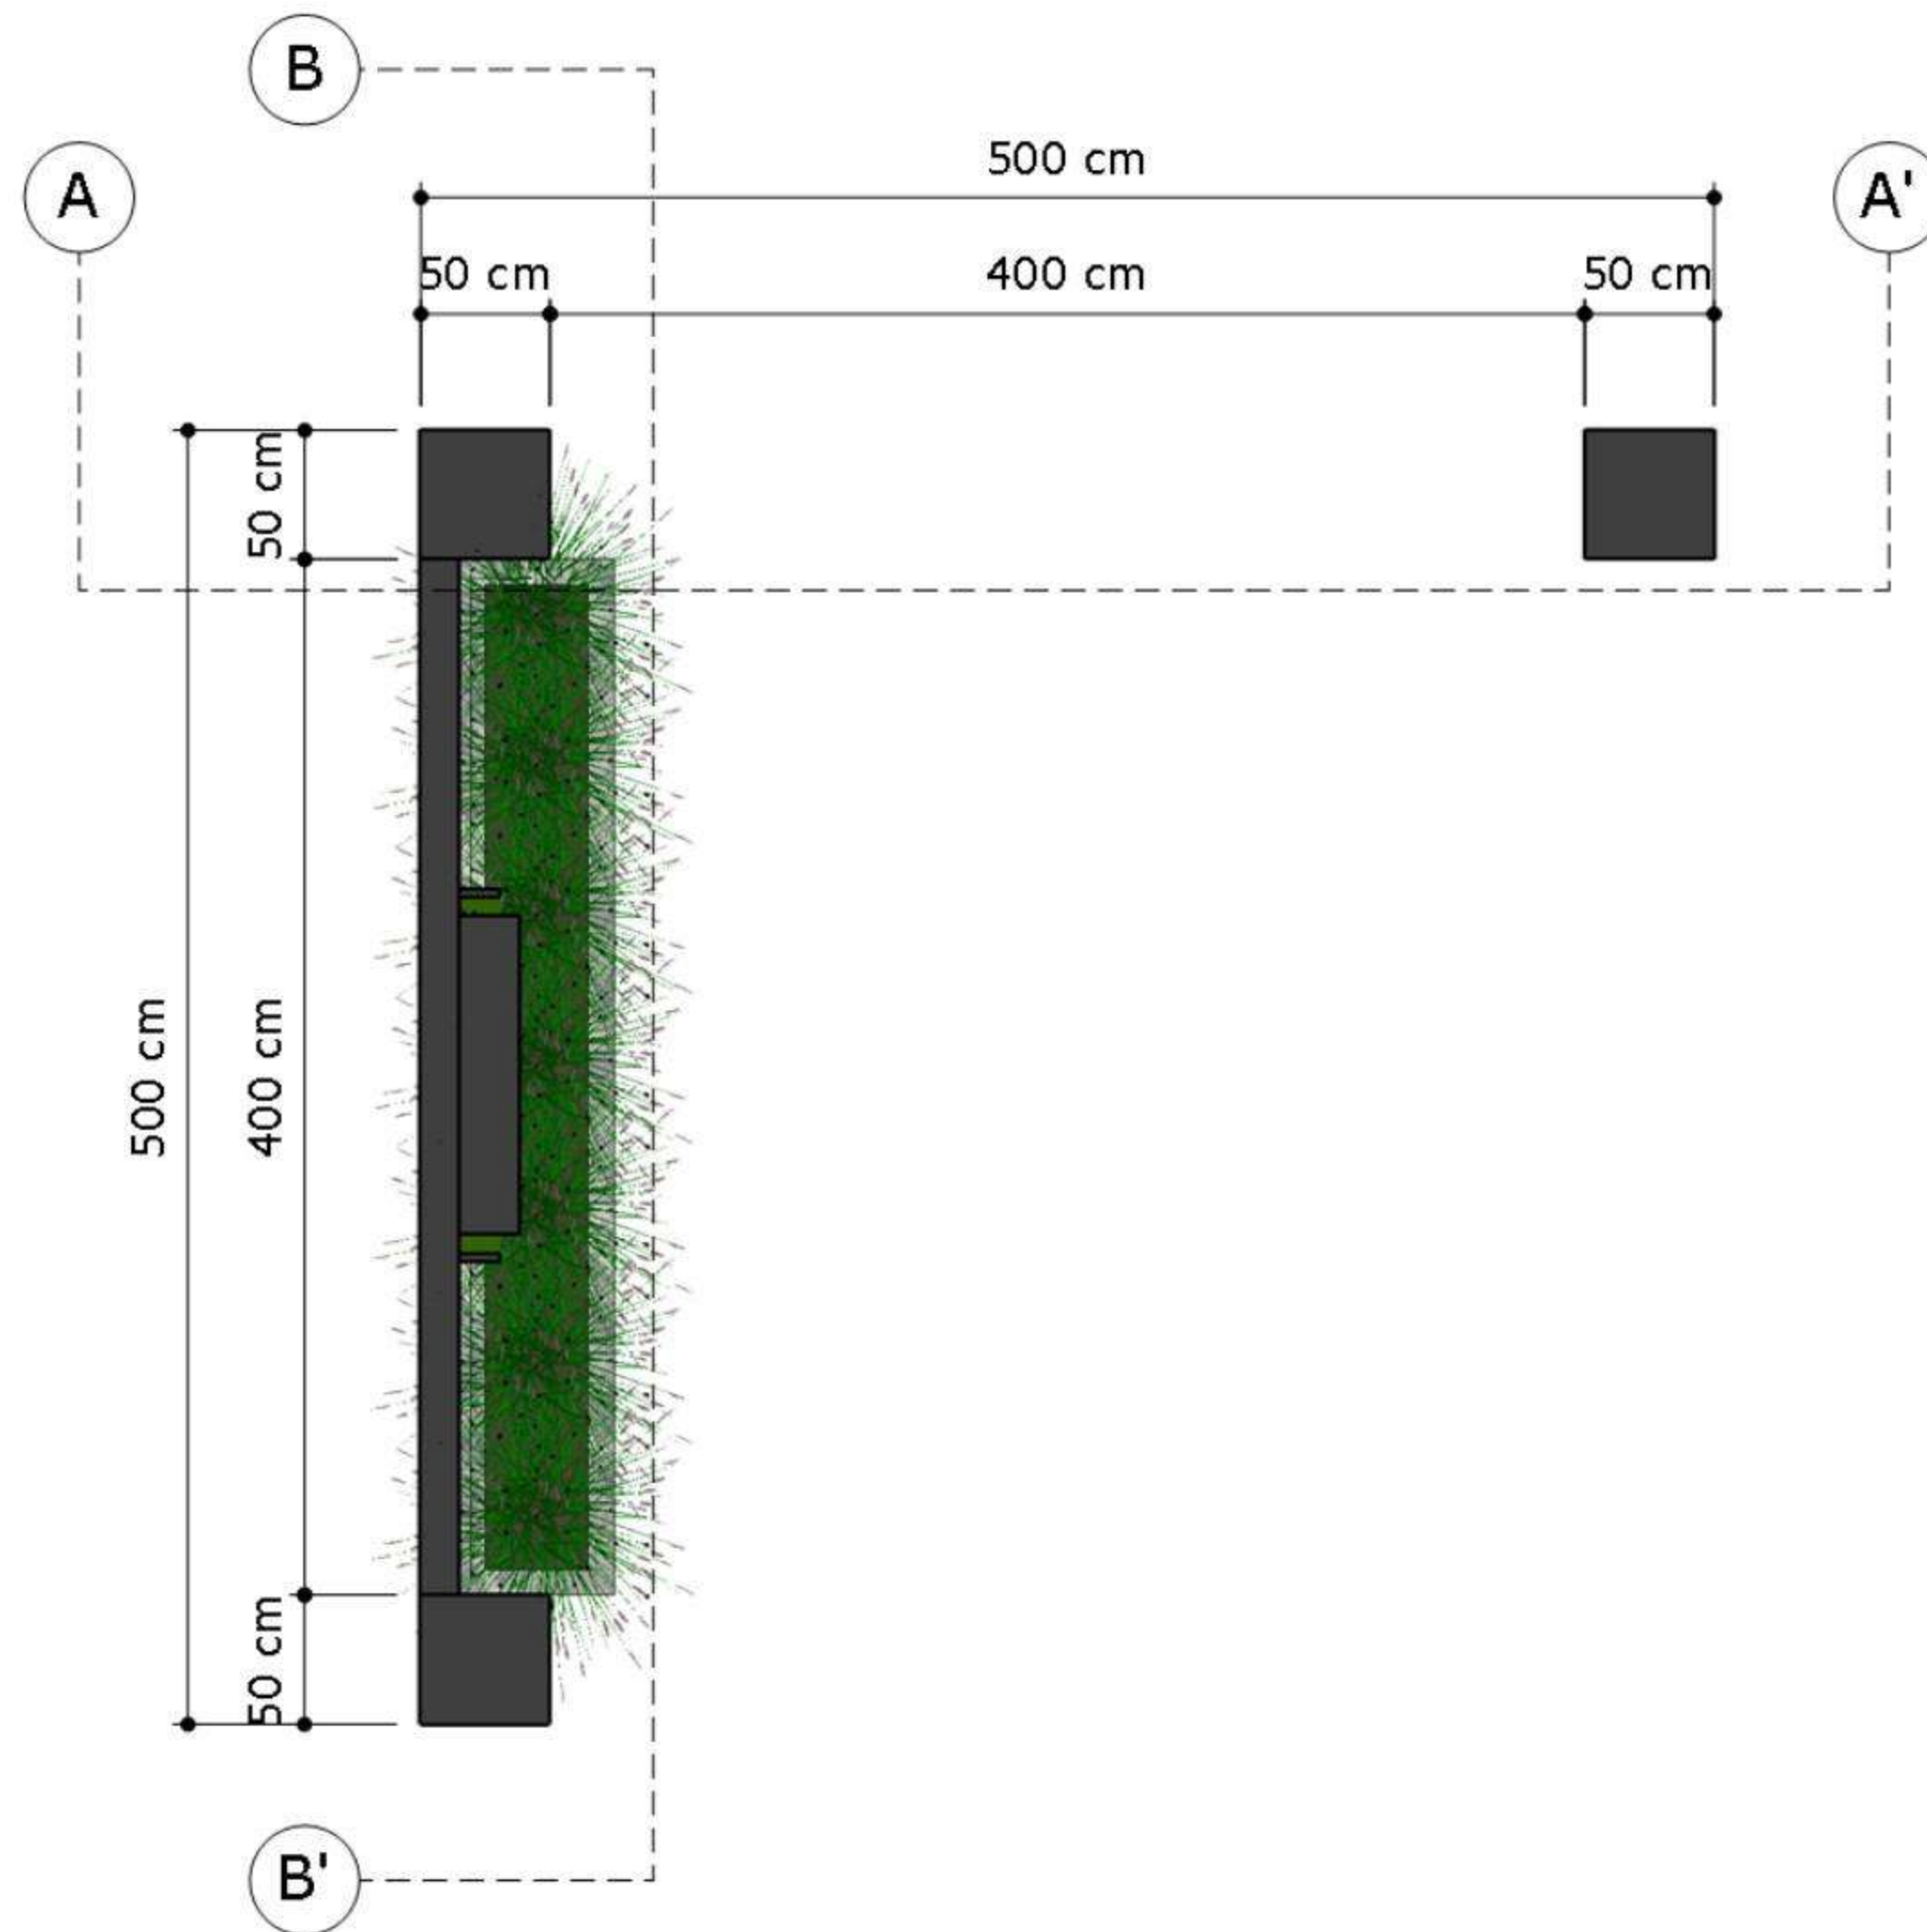


**FLOOR PLAN**  
1 : 30 SCALE

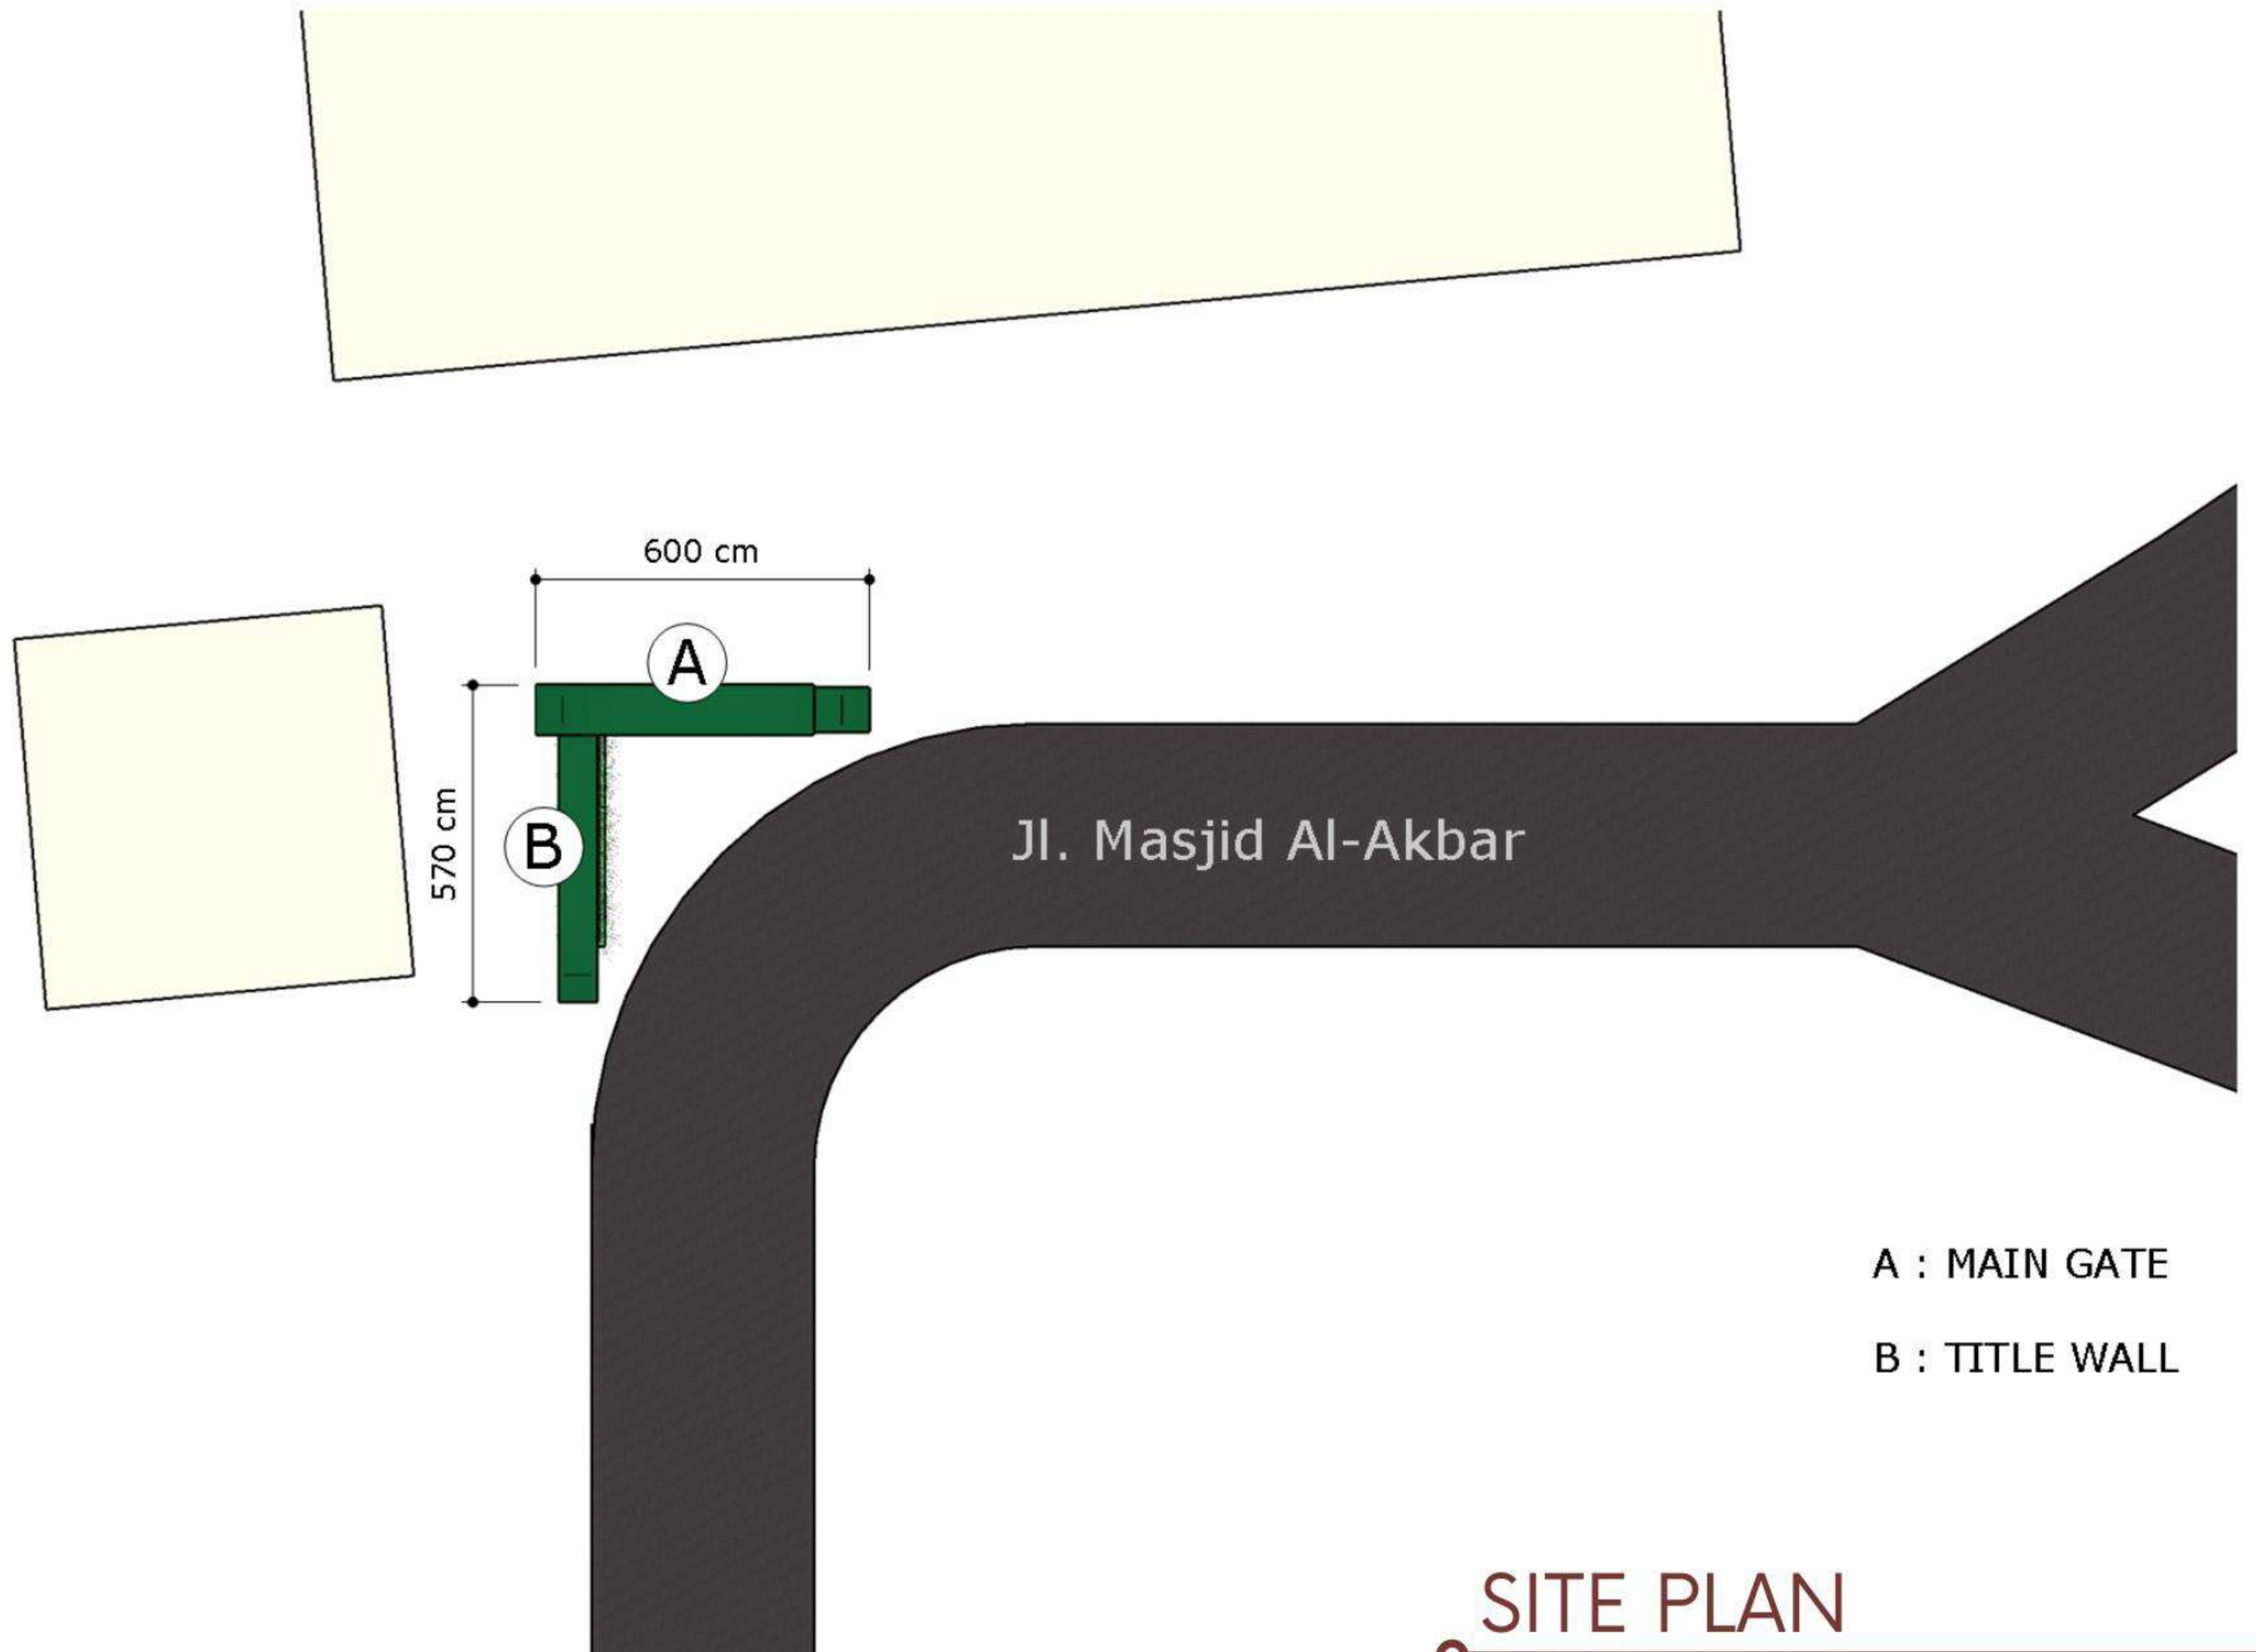


A : MAIN GATE

B : TITLE WALL


**SITE PLAN**  
1 : 100 SCALE

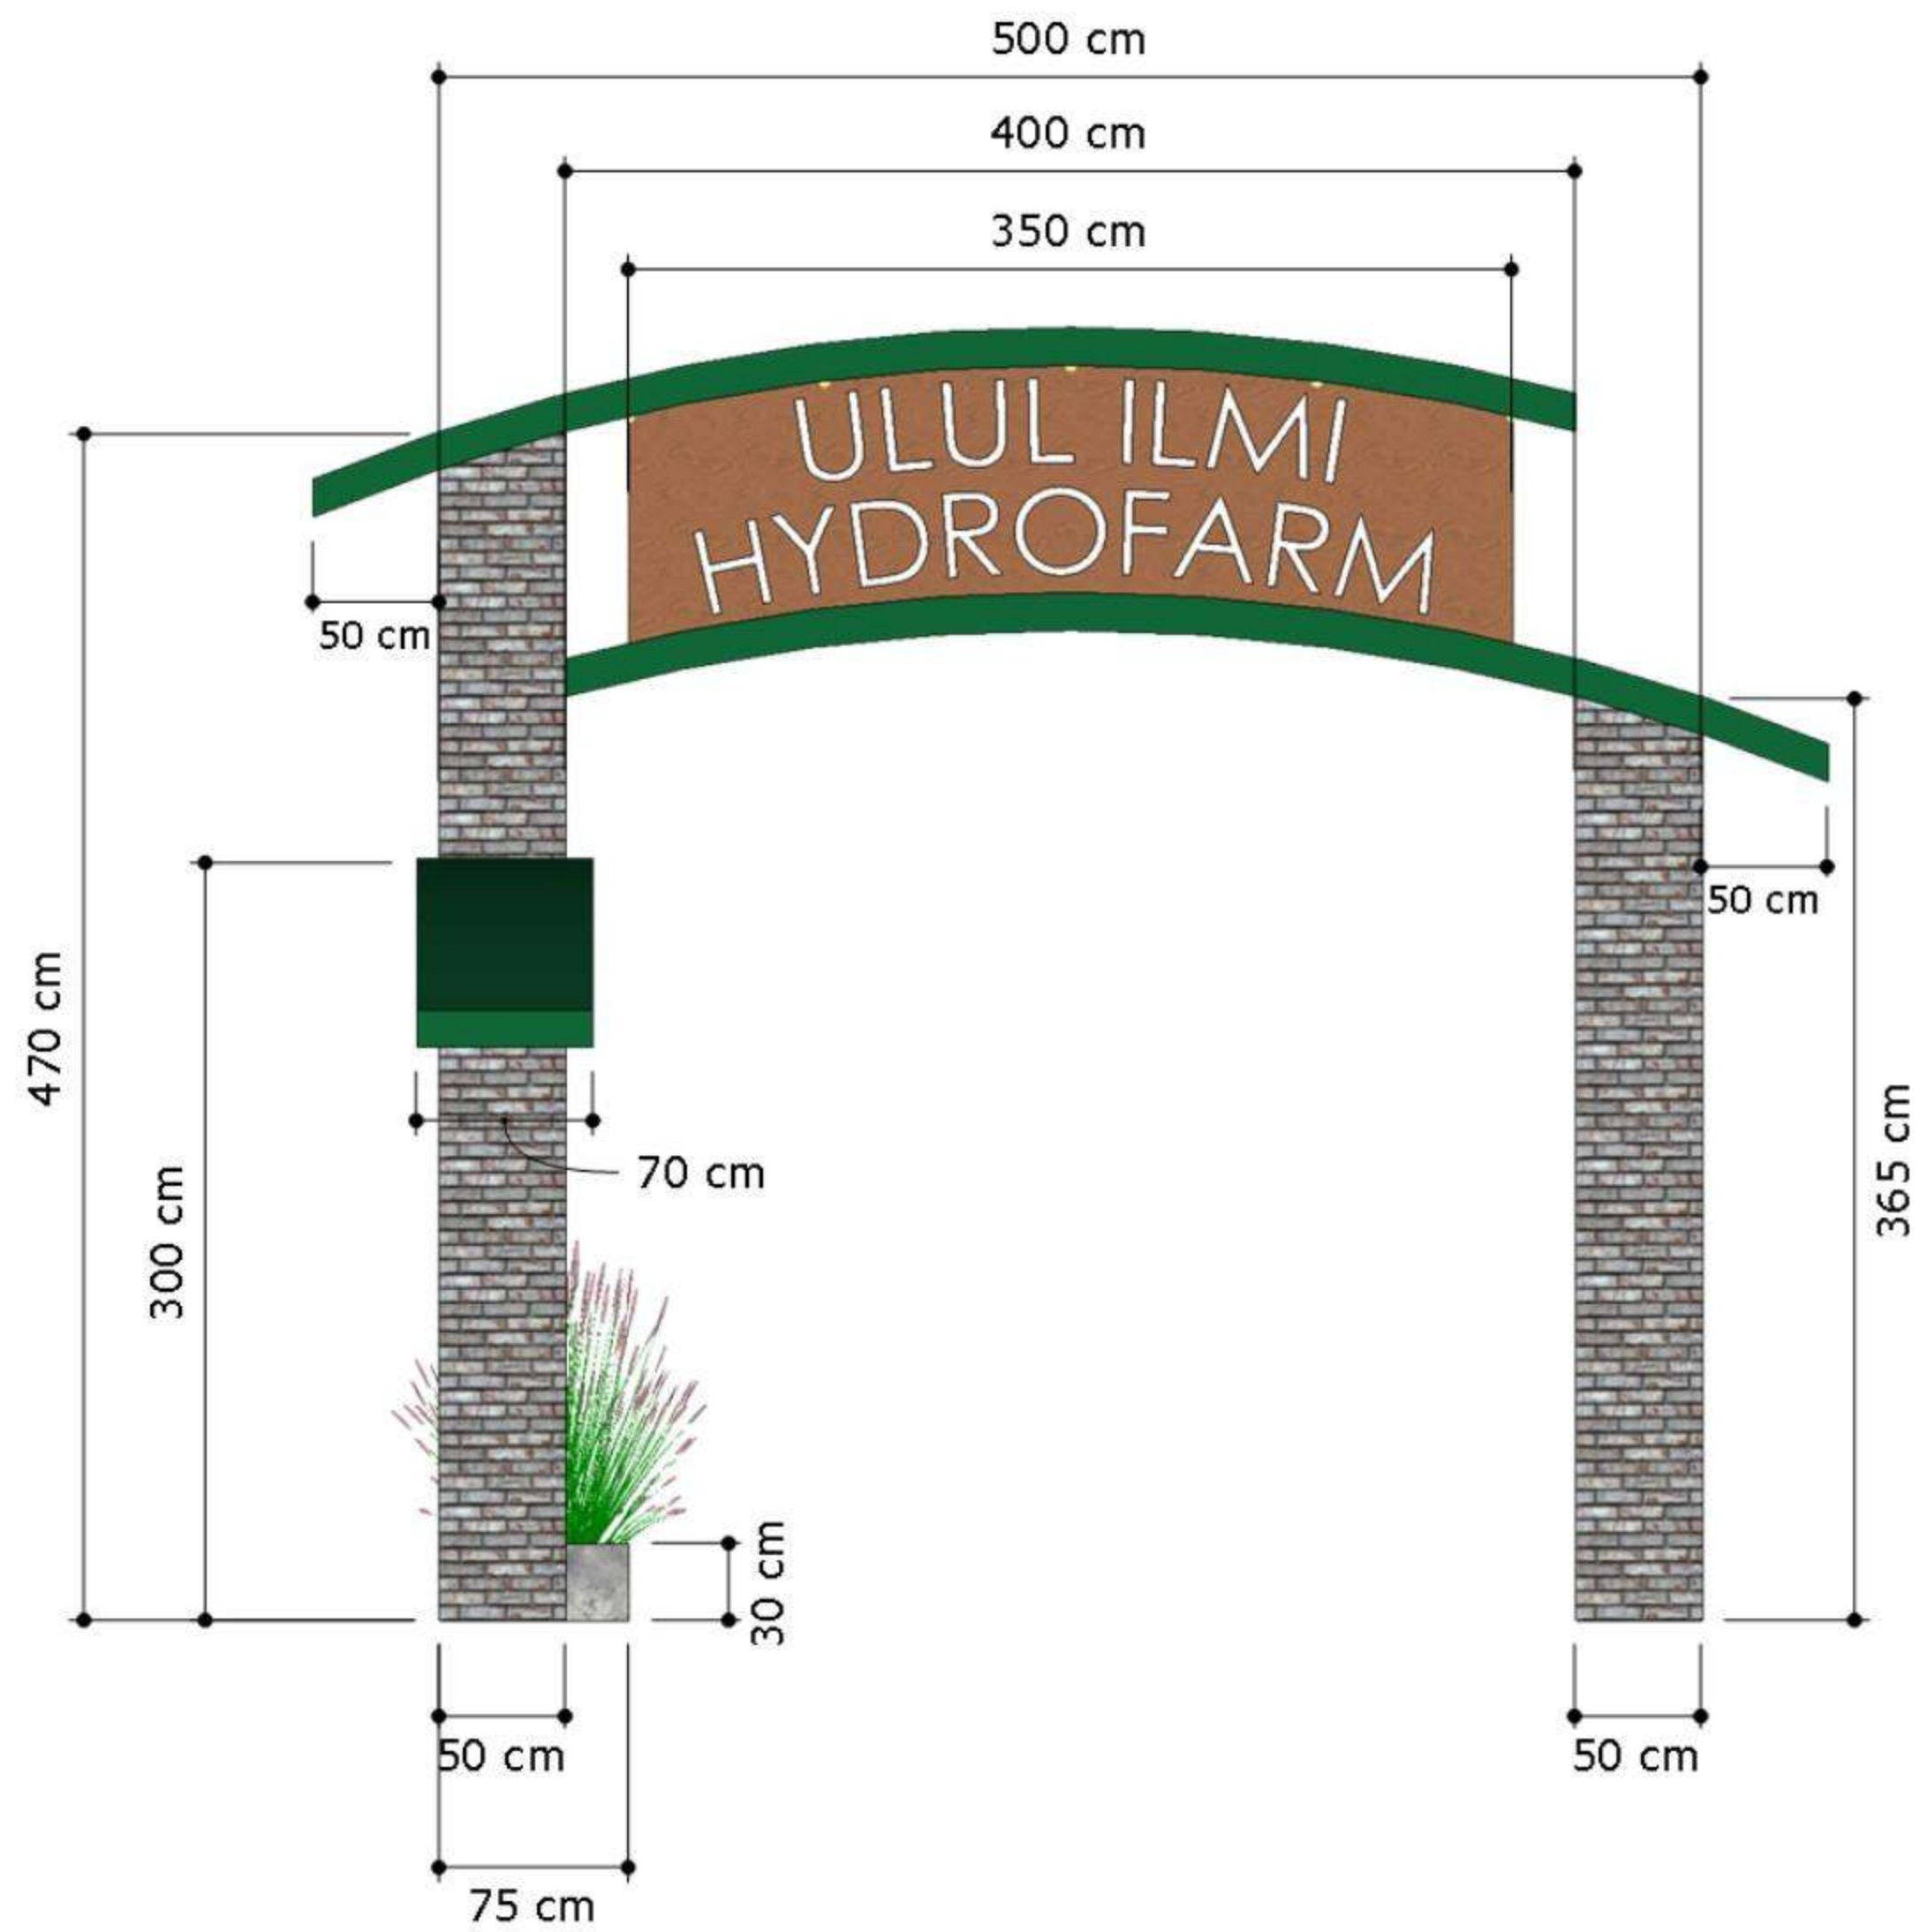


FRONT VIEW  
1 : 30 SCALE

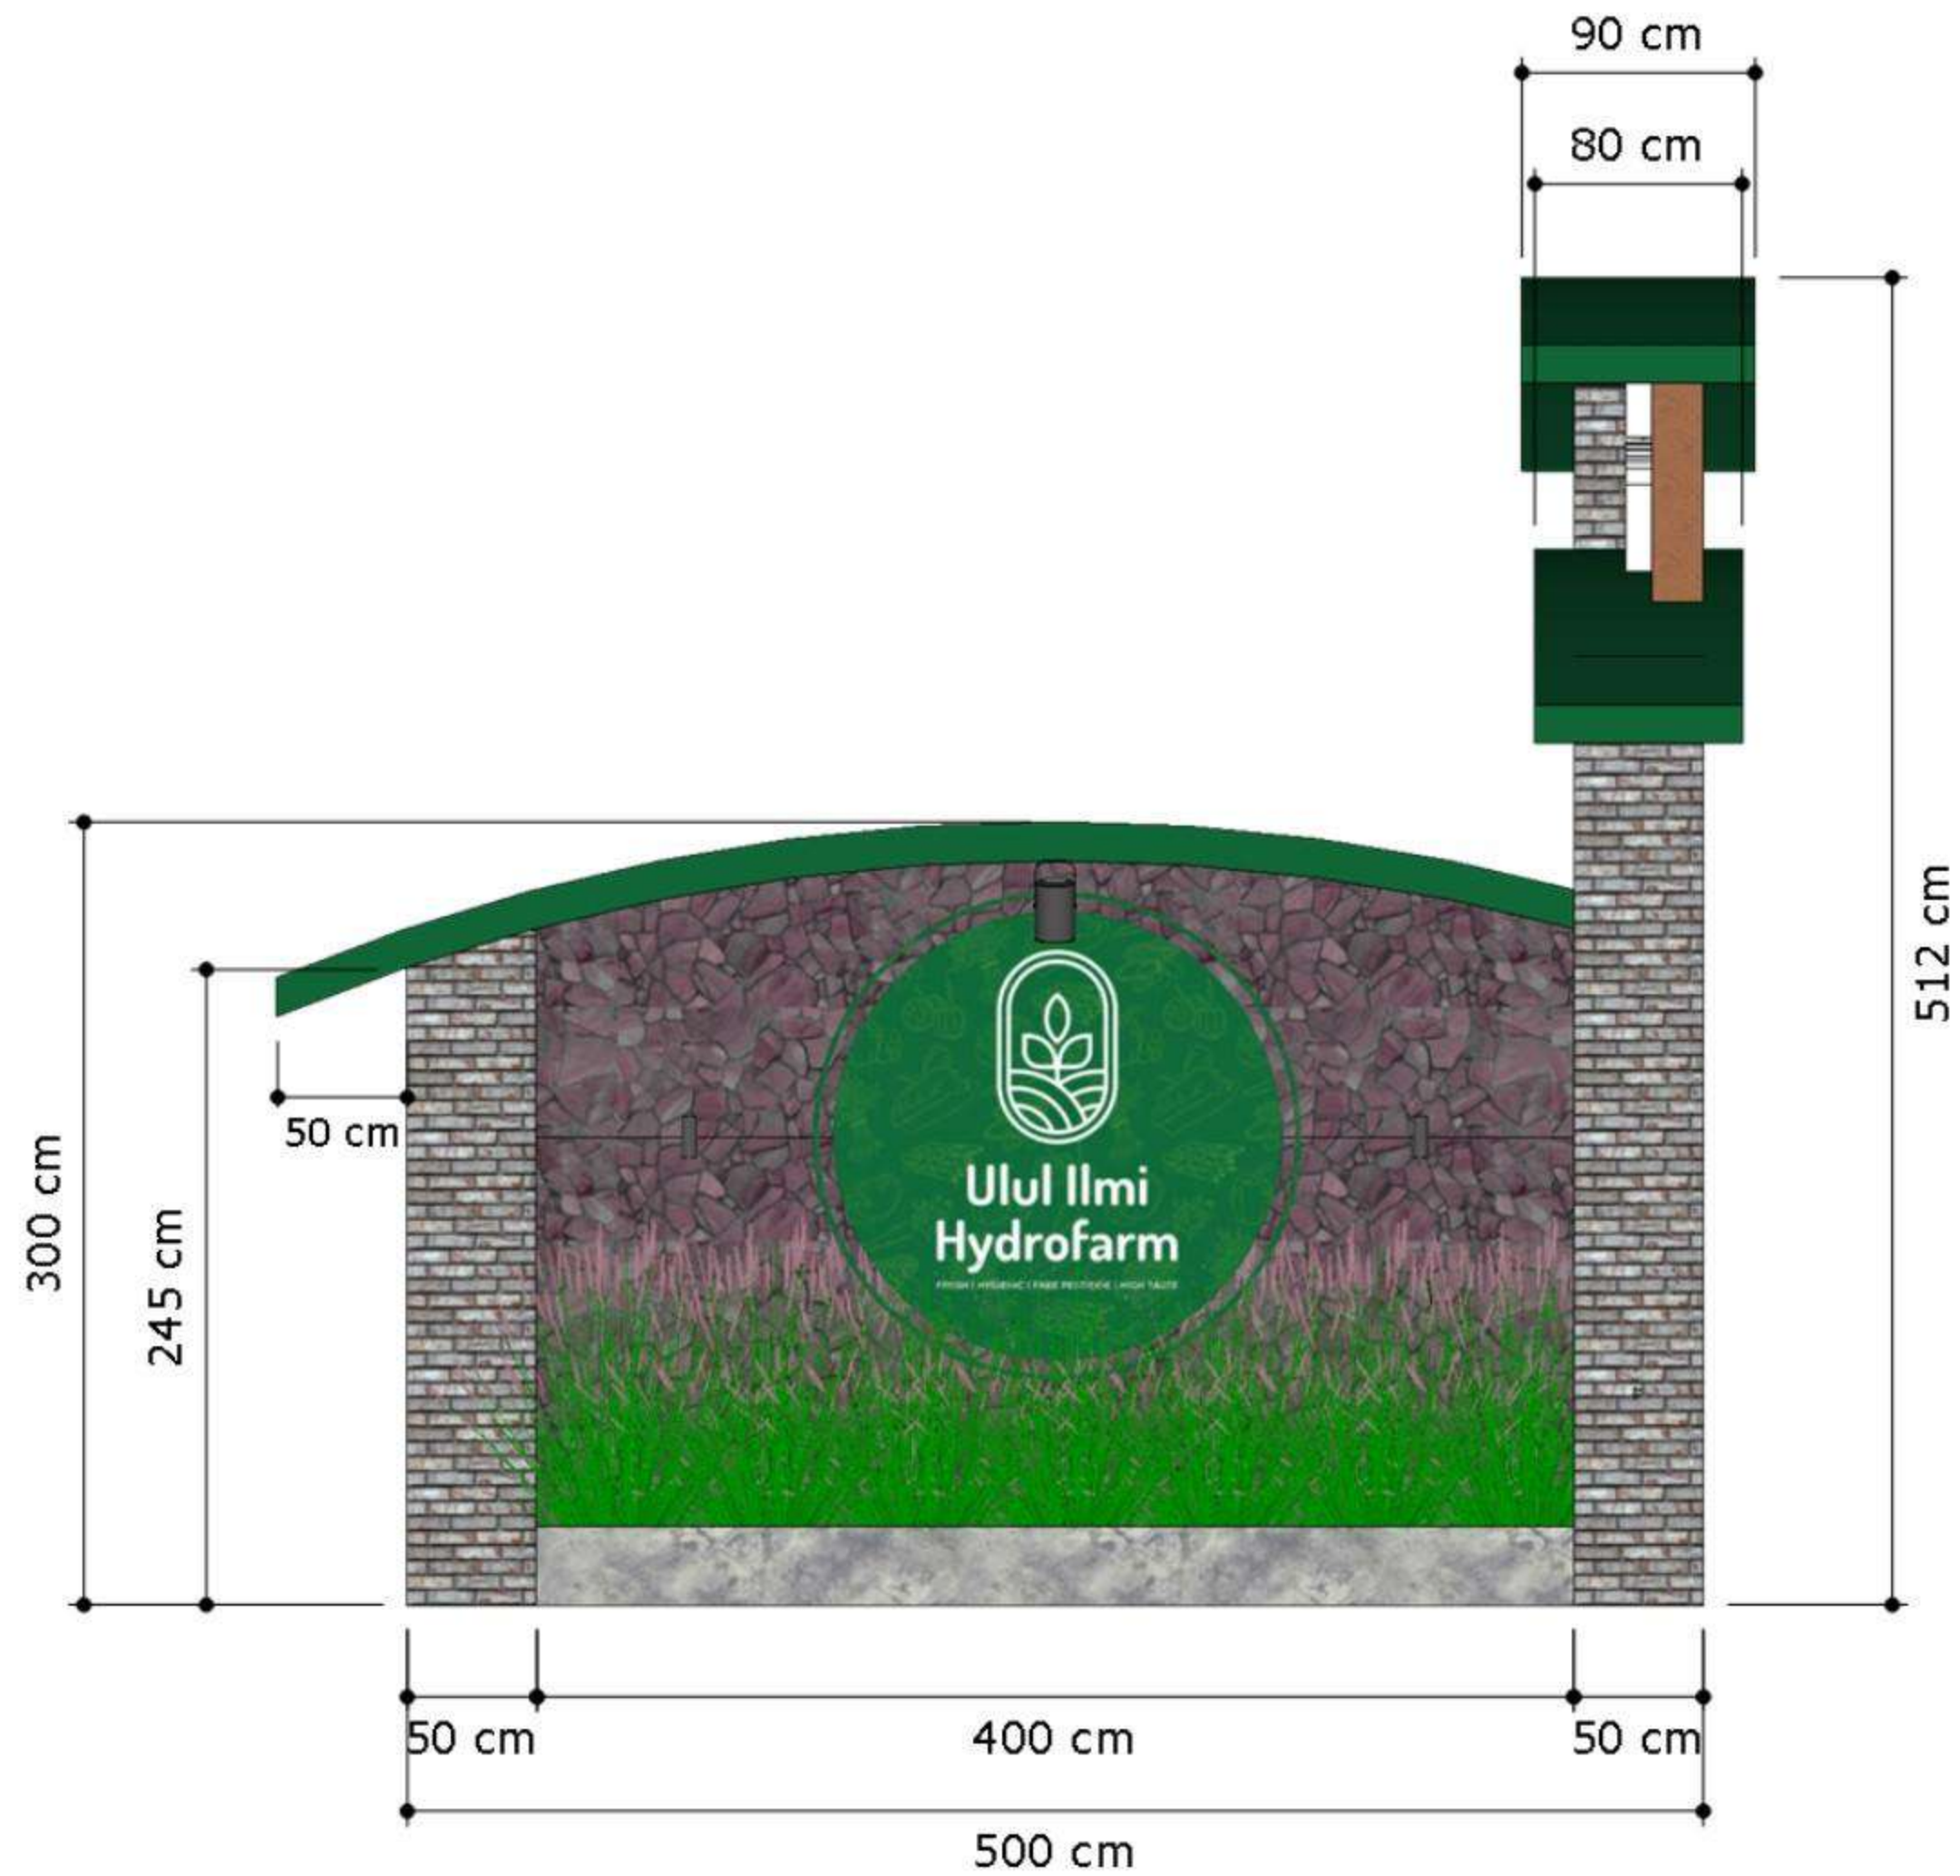


**SIDE VIEW**  
1 : 30 SCALE

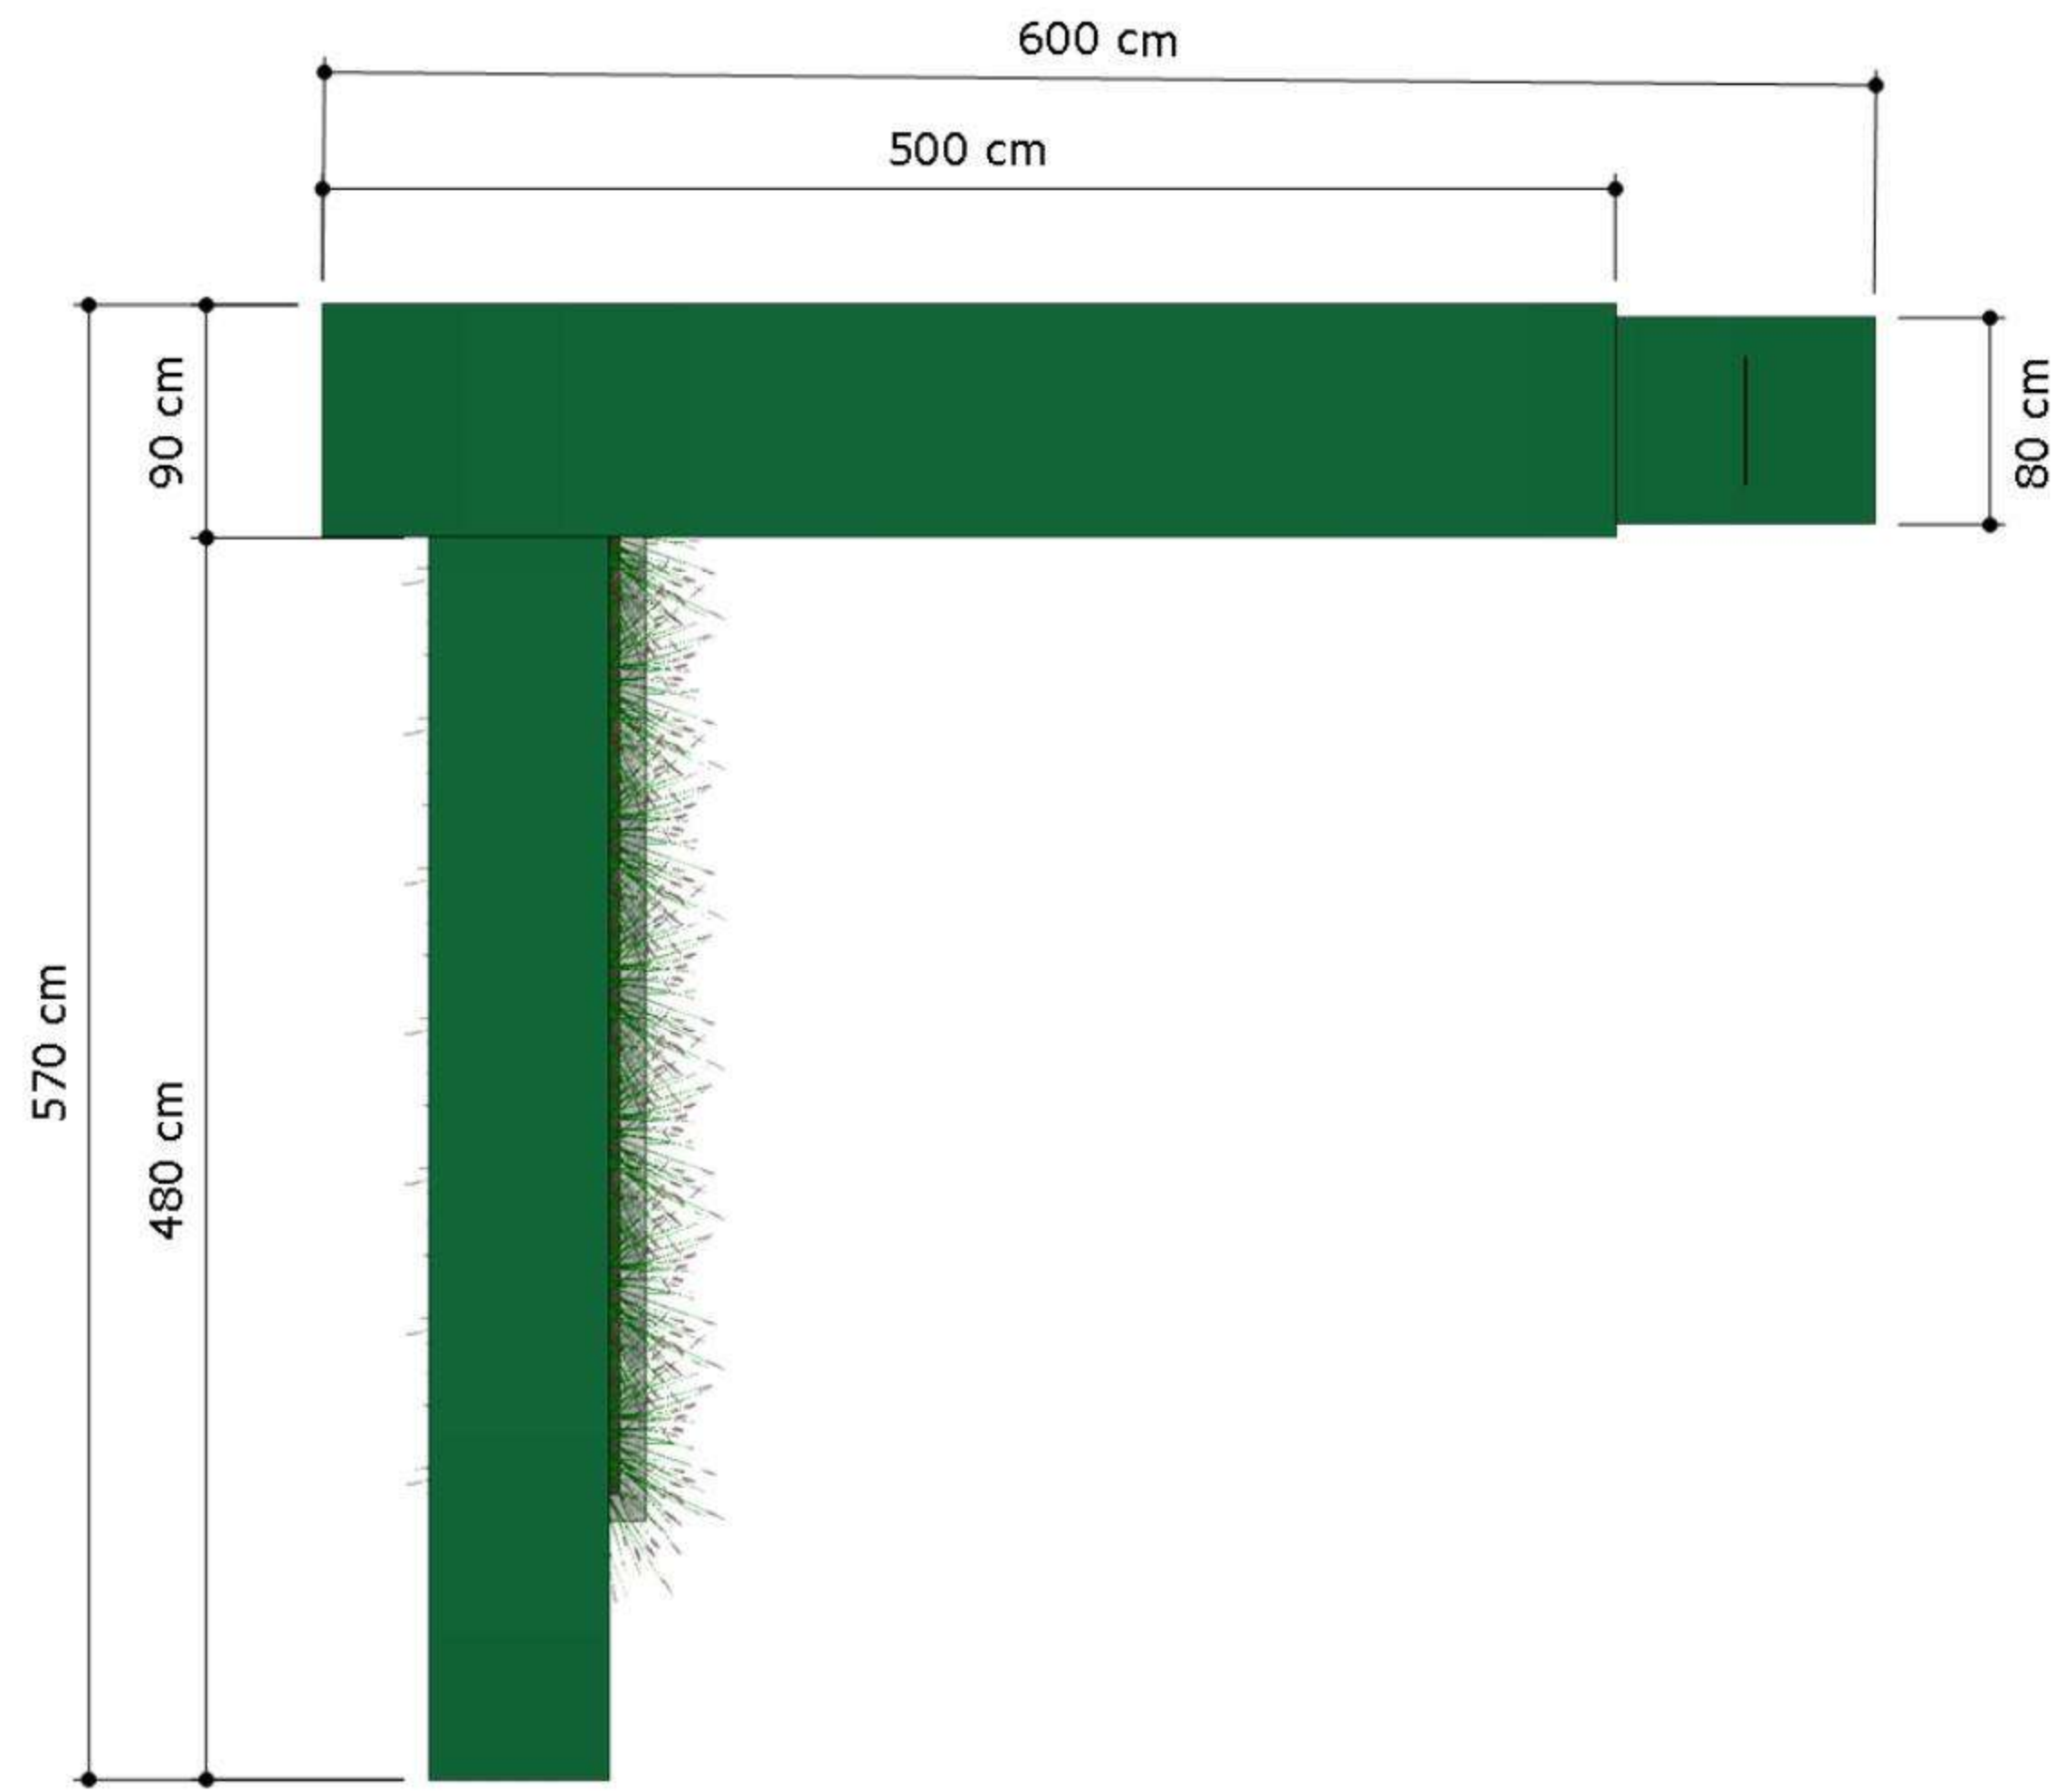


TOP VIEW  
1 : 30 SCALE

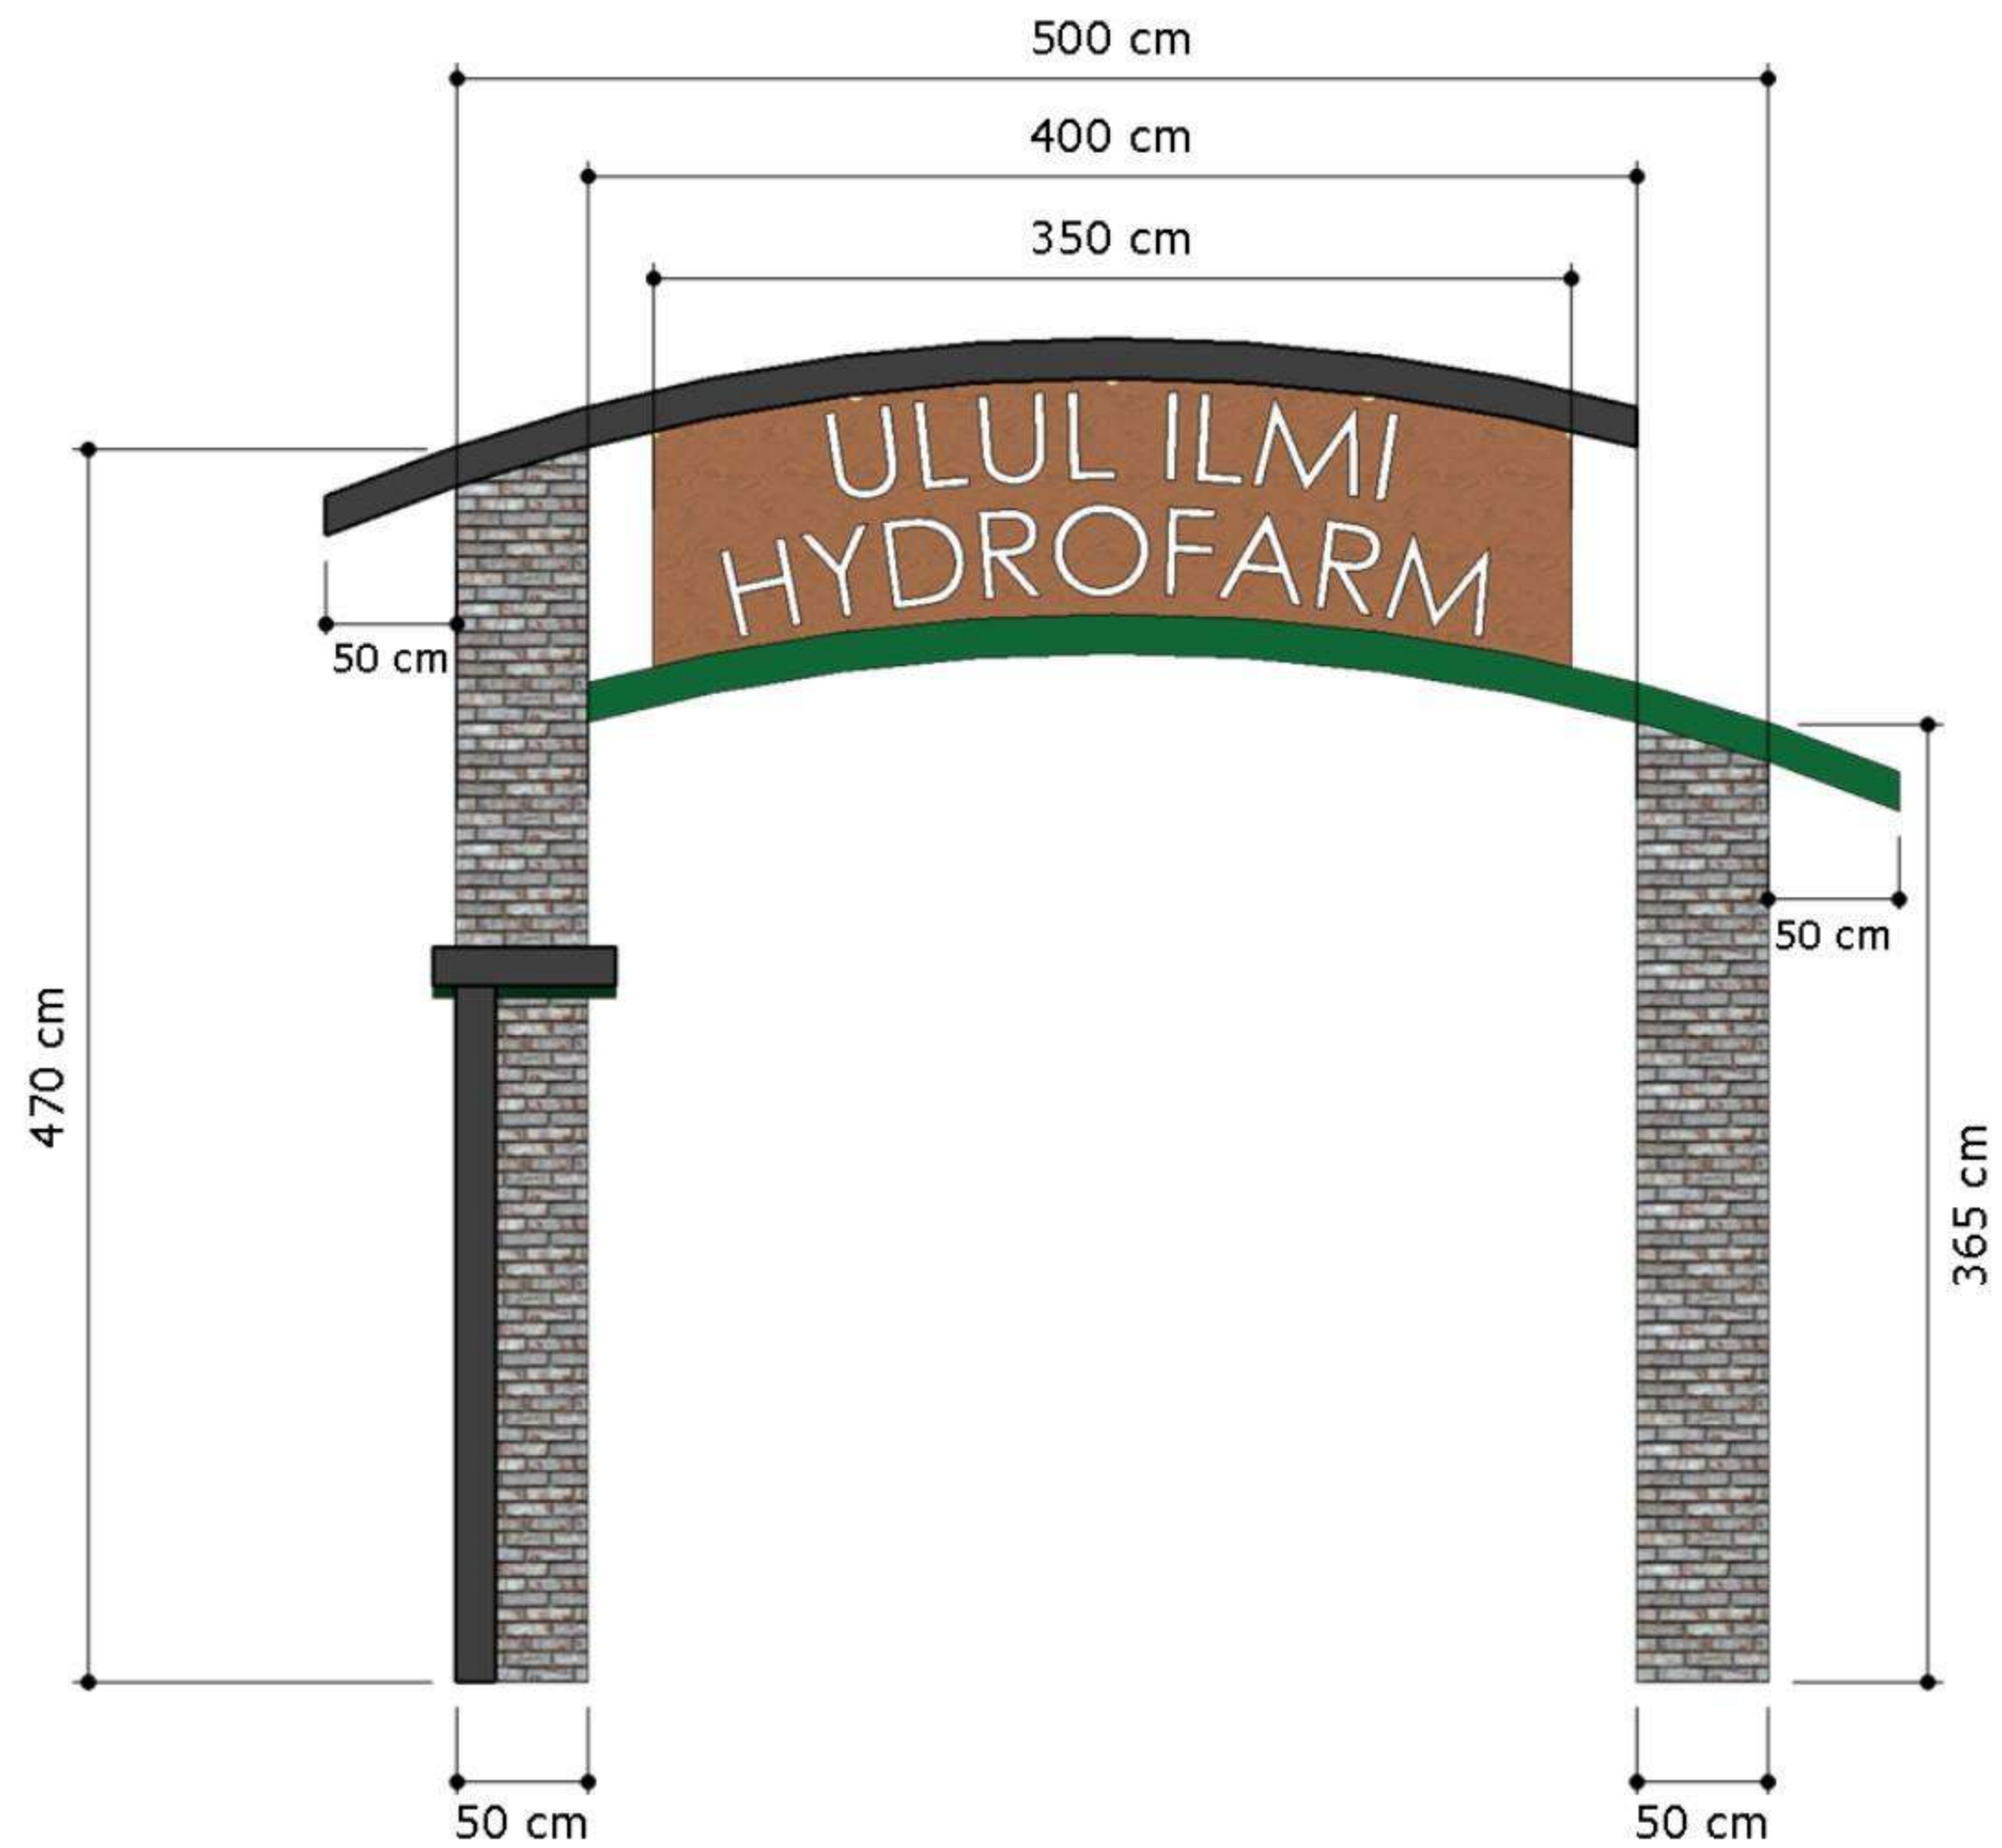

A SECTION  
1 : 30 SCALE

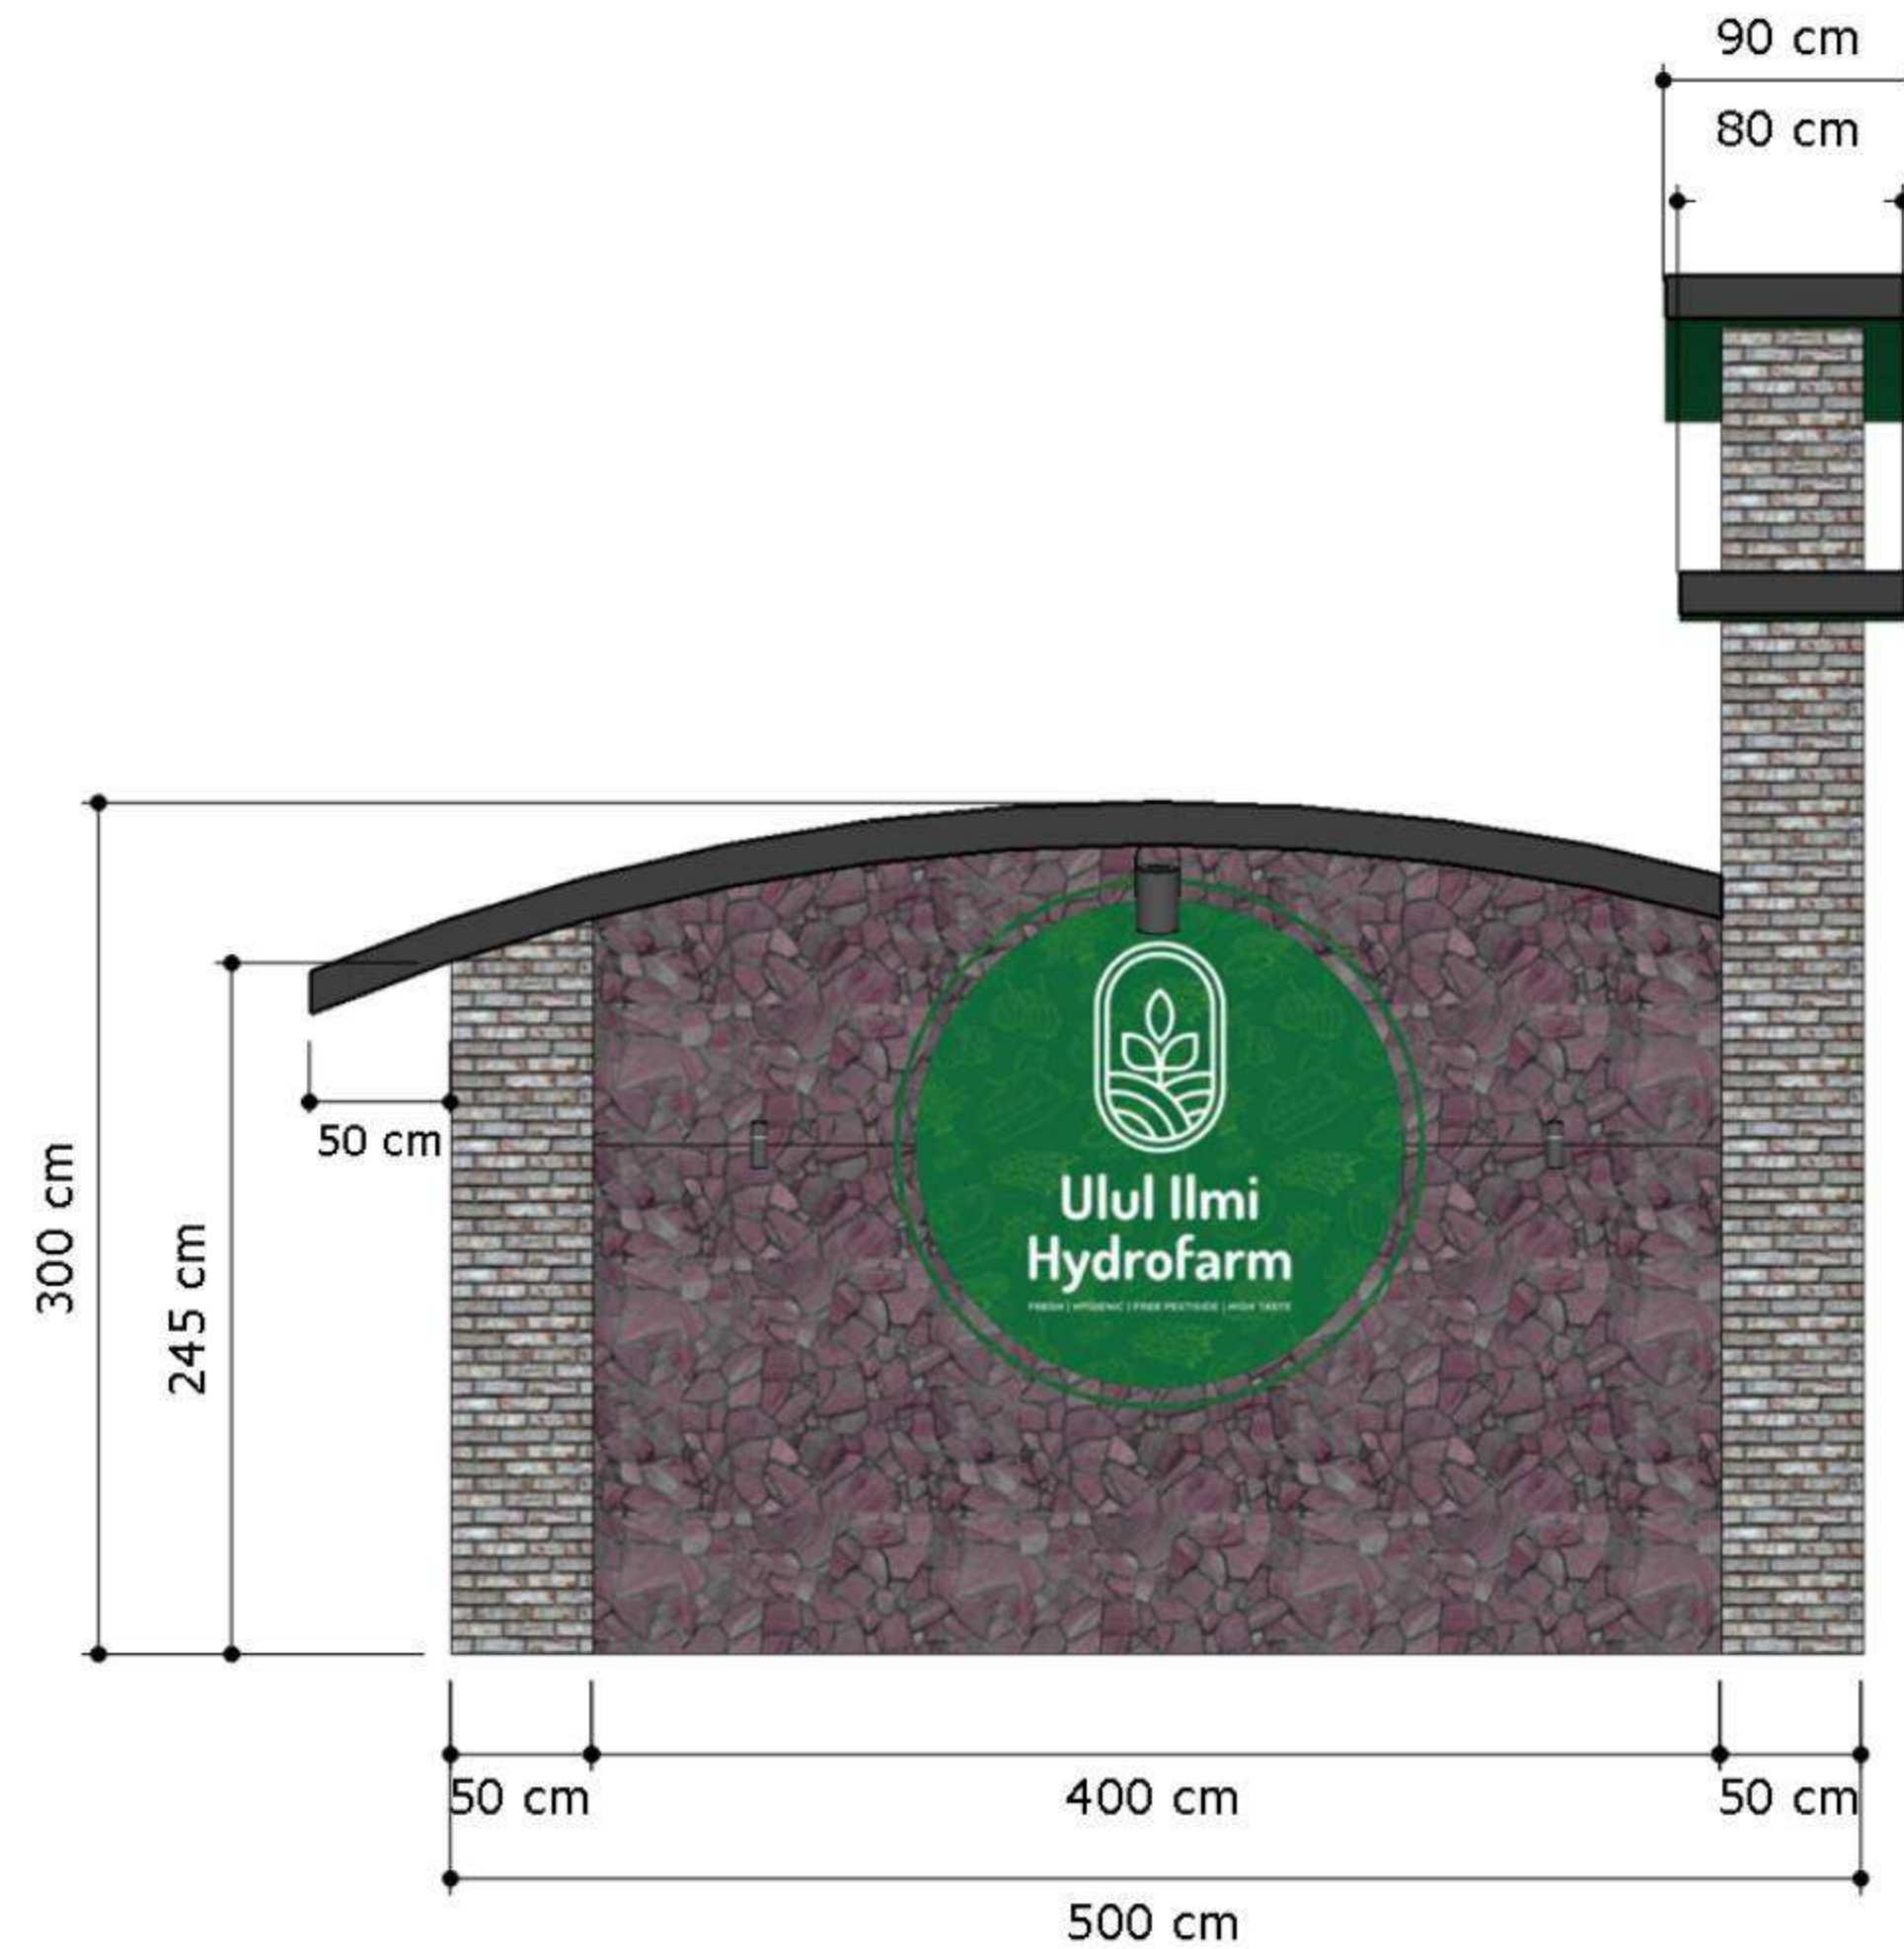

**B SECTION**  
1 : 30 SCALE


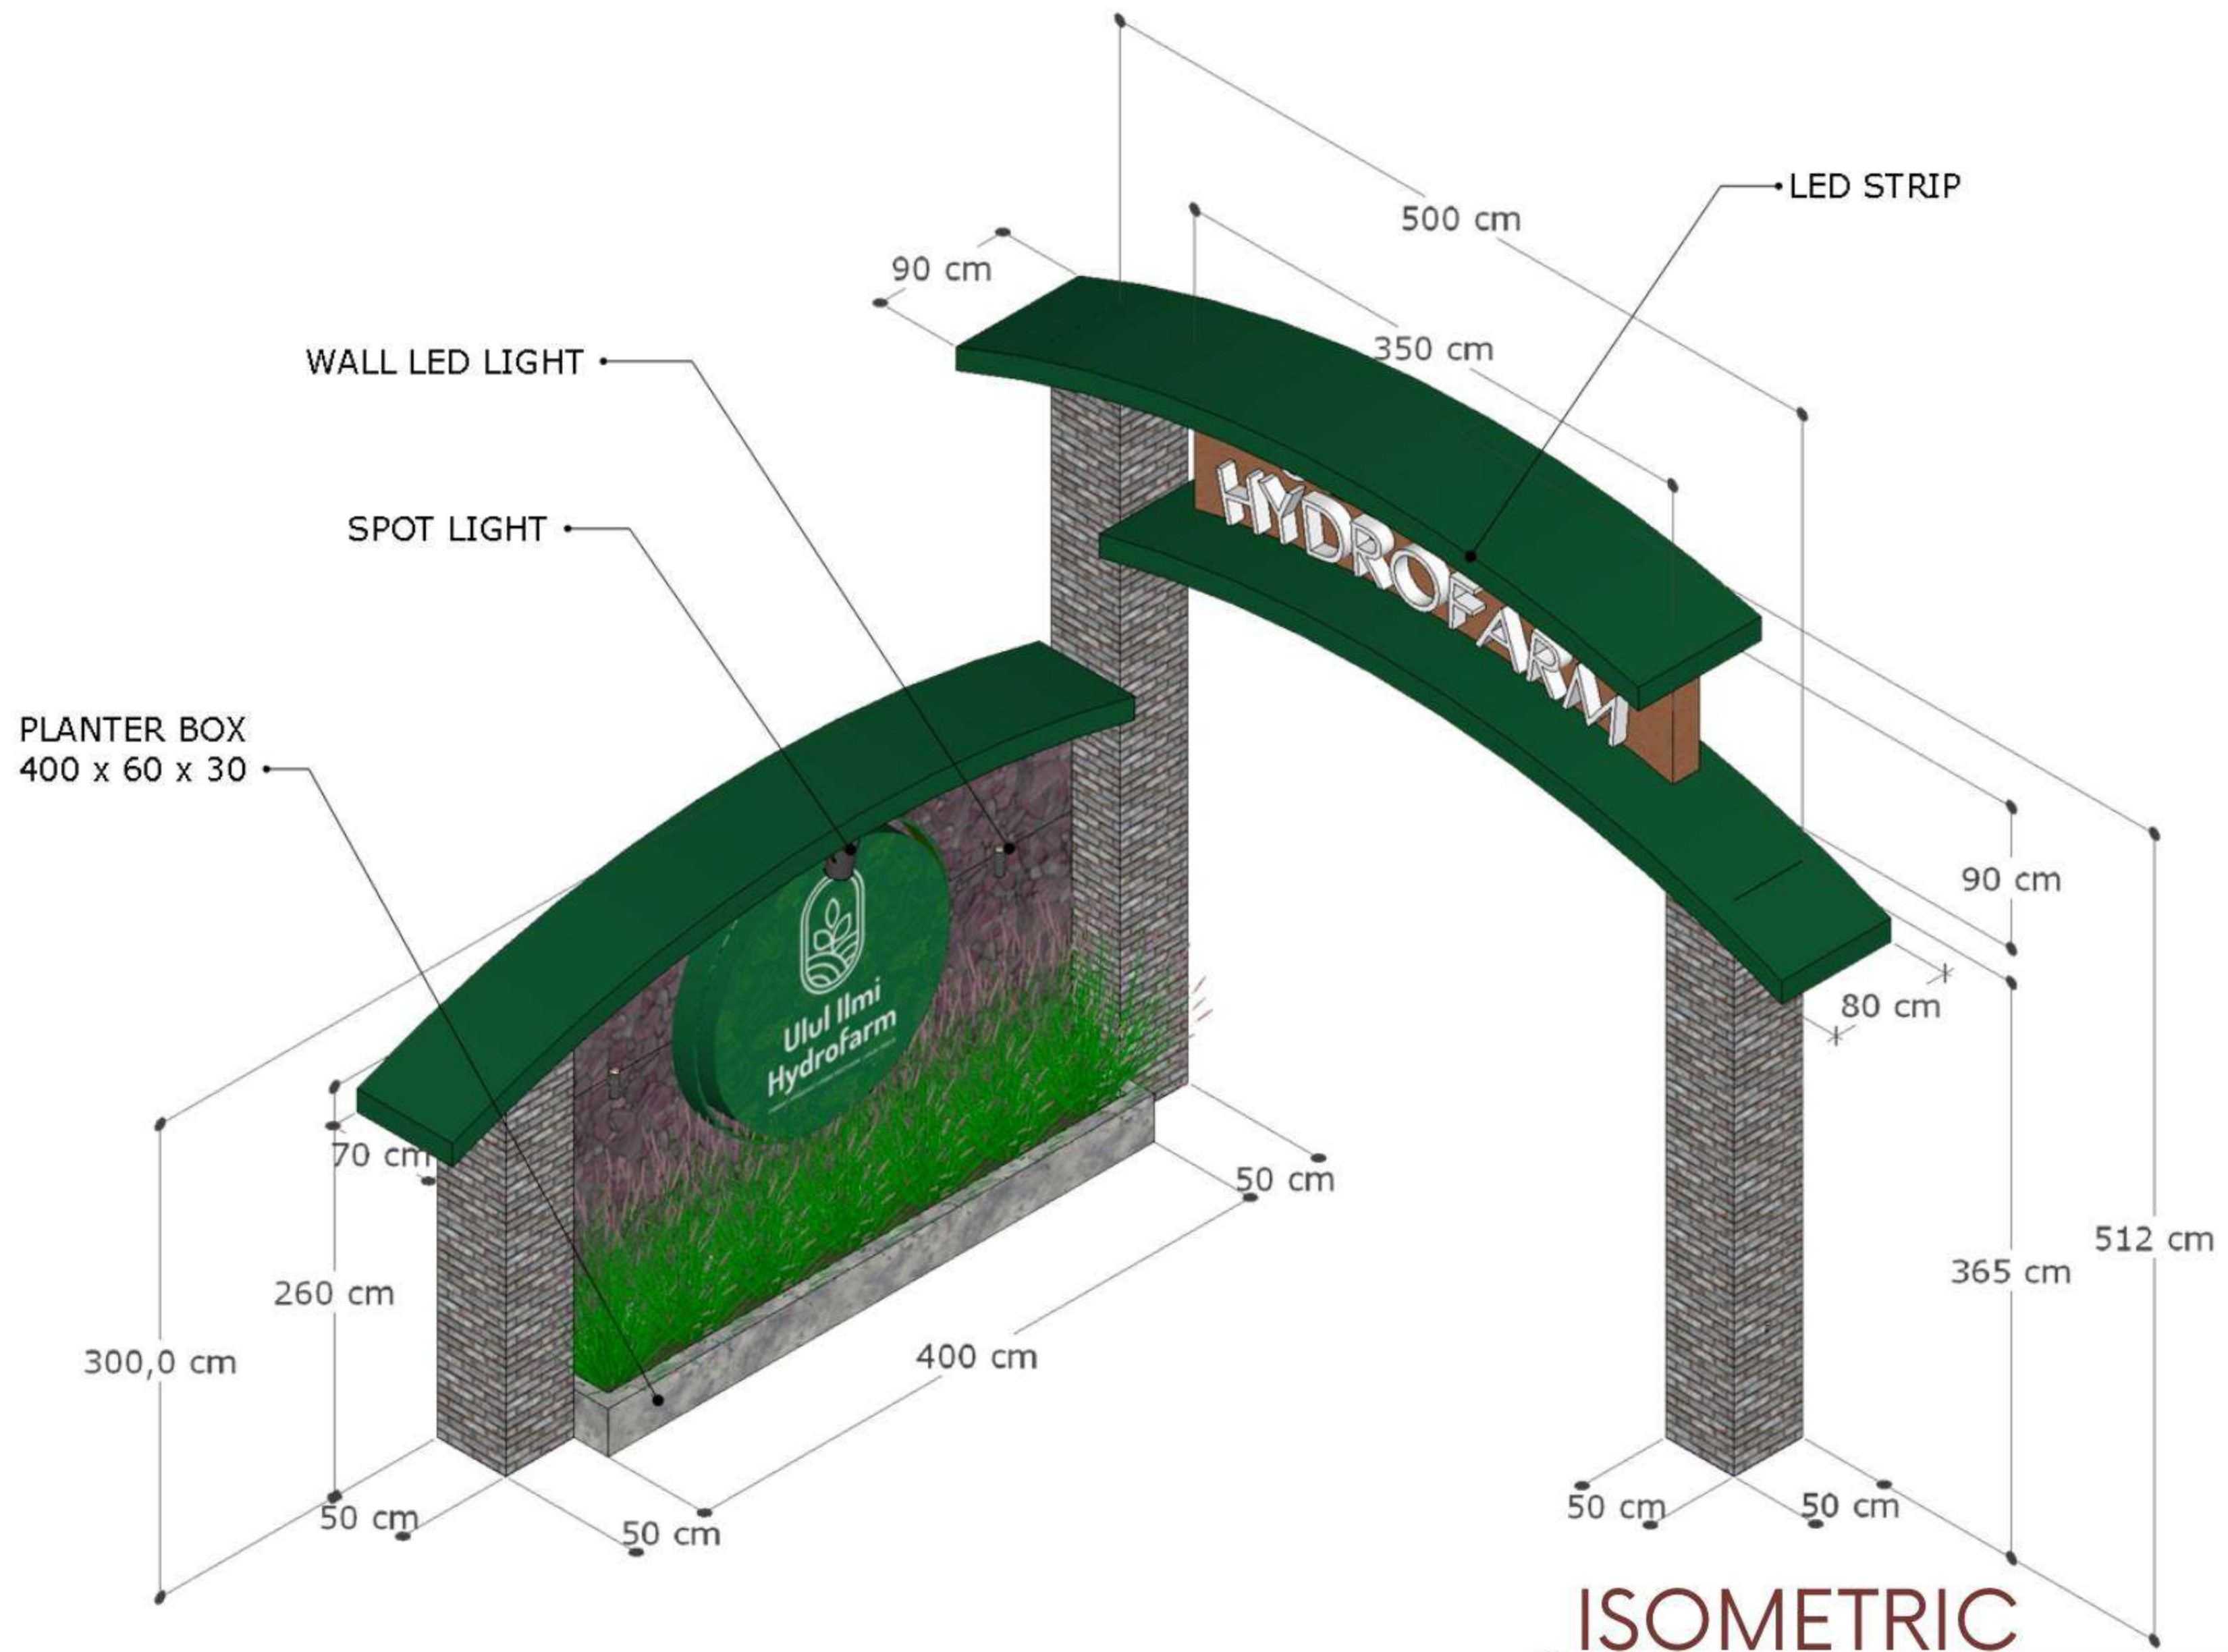


ISOMETRIC  
1 : 30 SCALE





STAINLESS 4"

EXPOSED CONWOOD

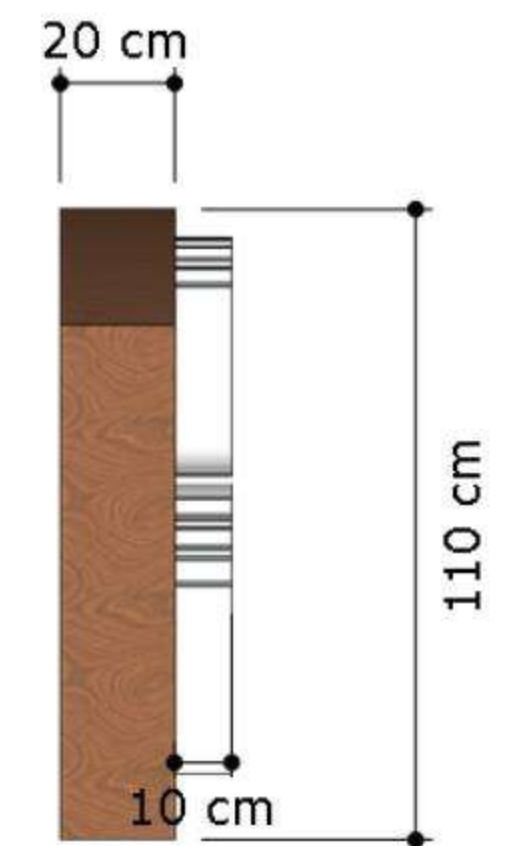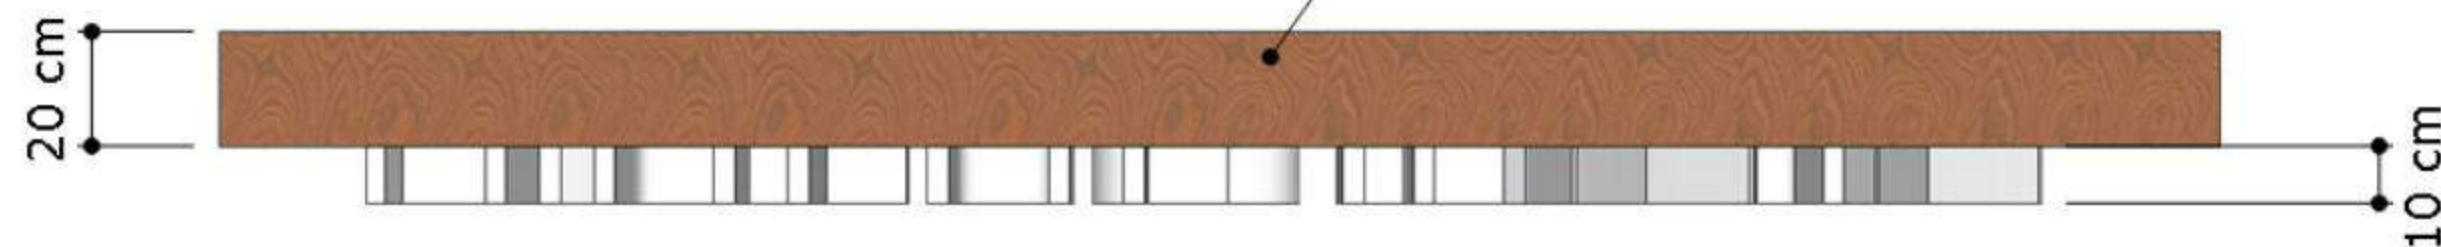

NAME BOARD DETAIL  
1 : 15 SCALE

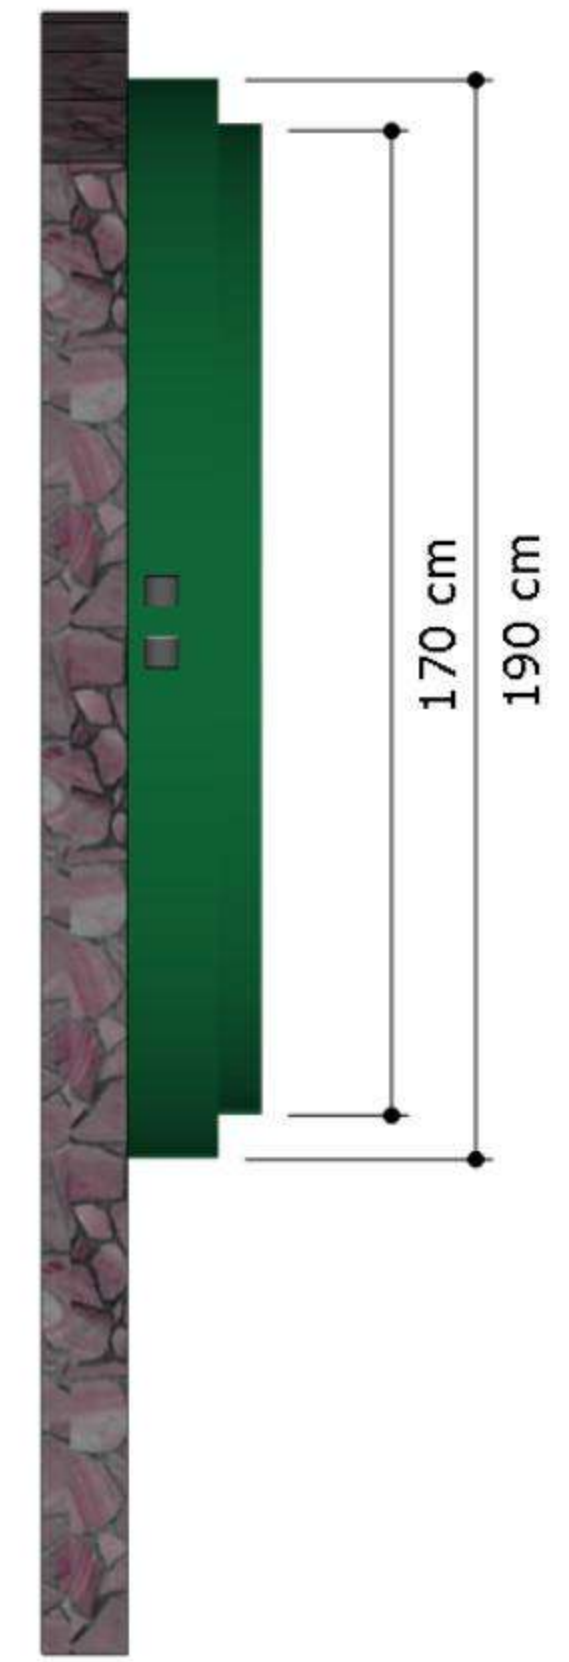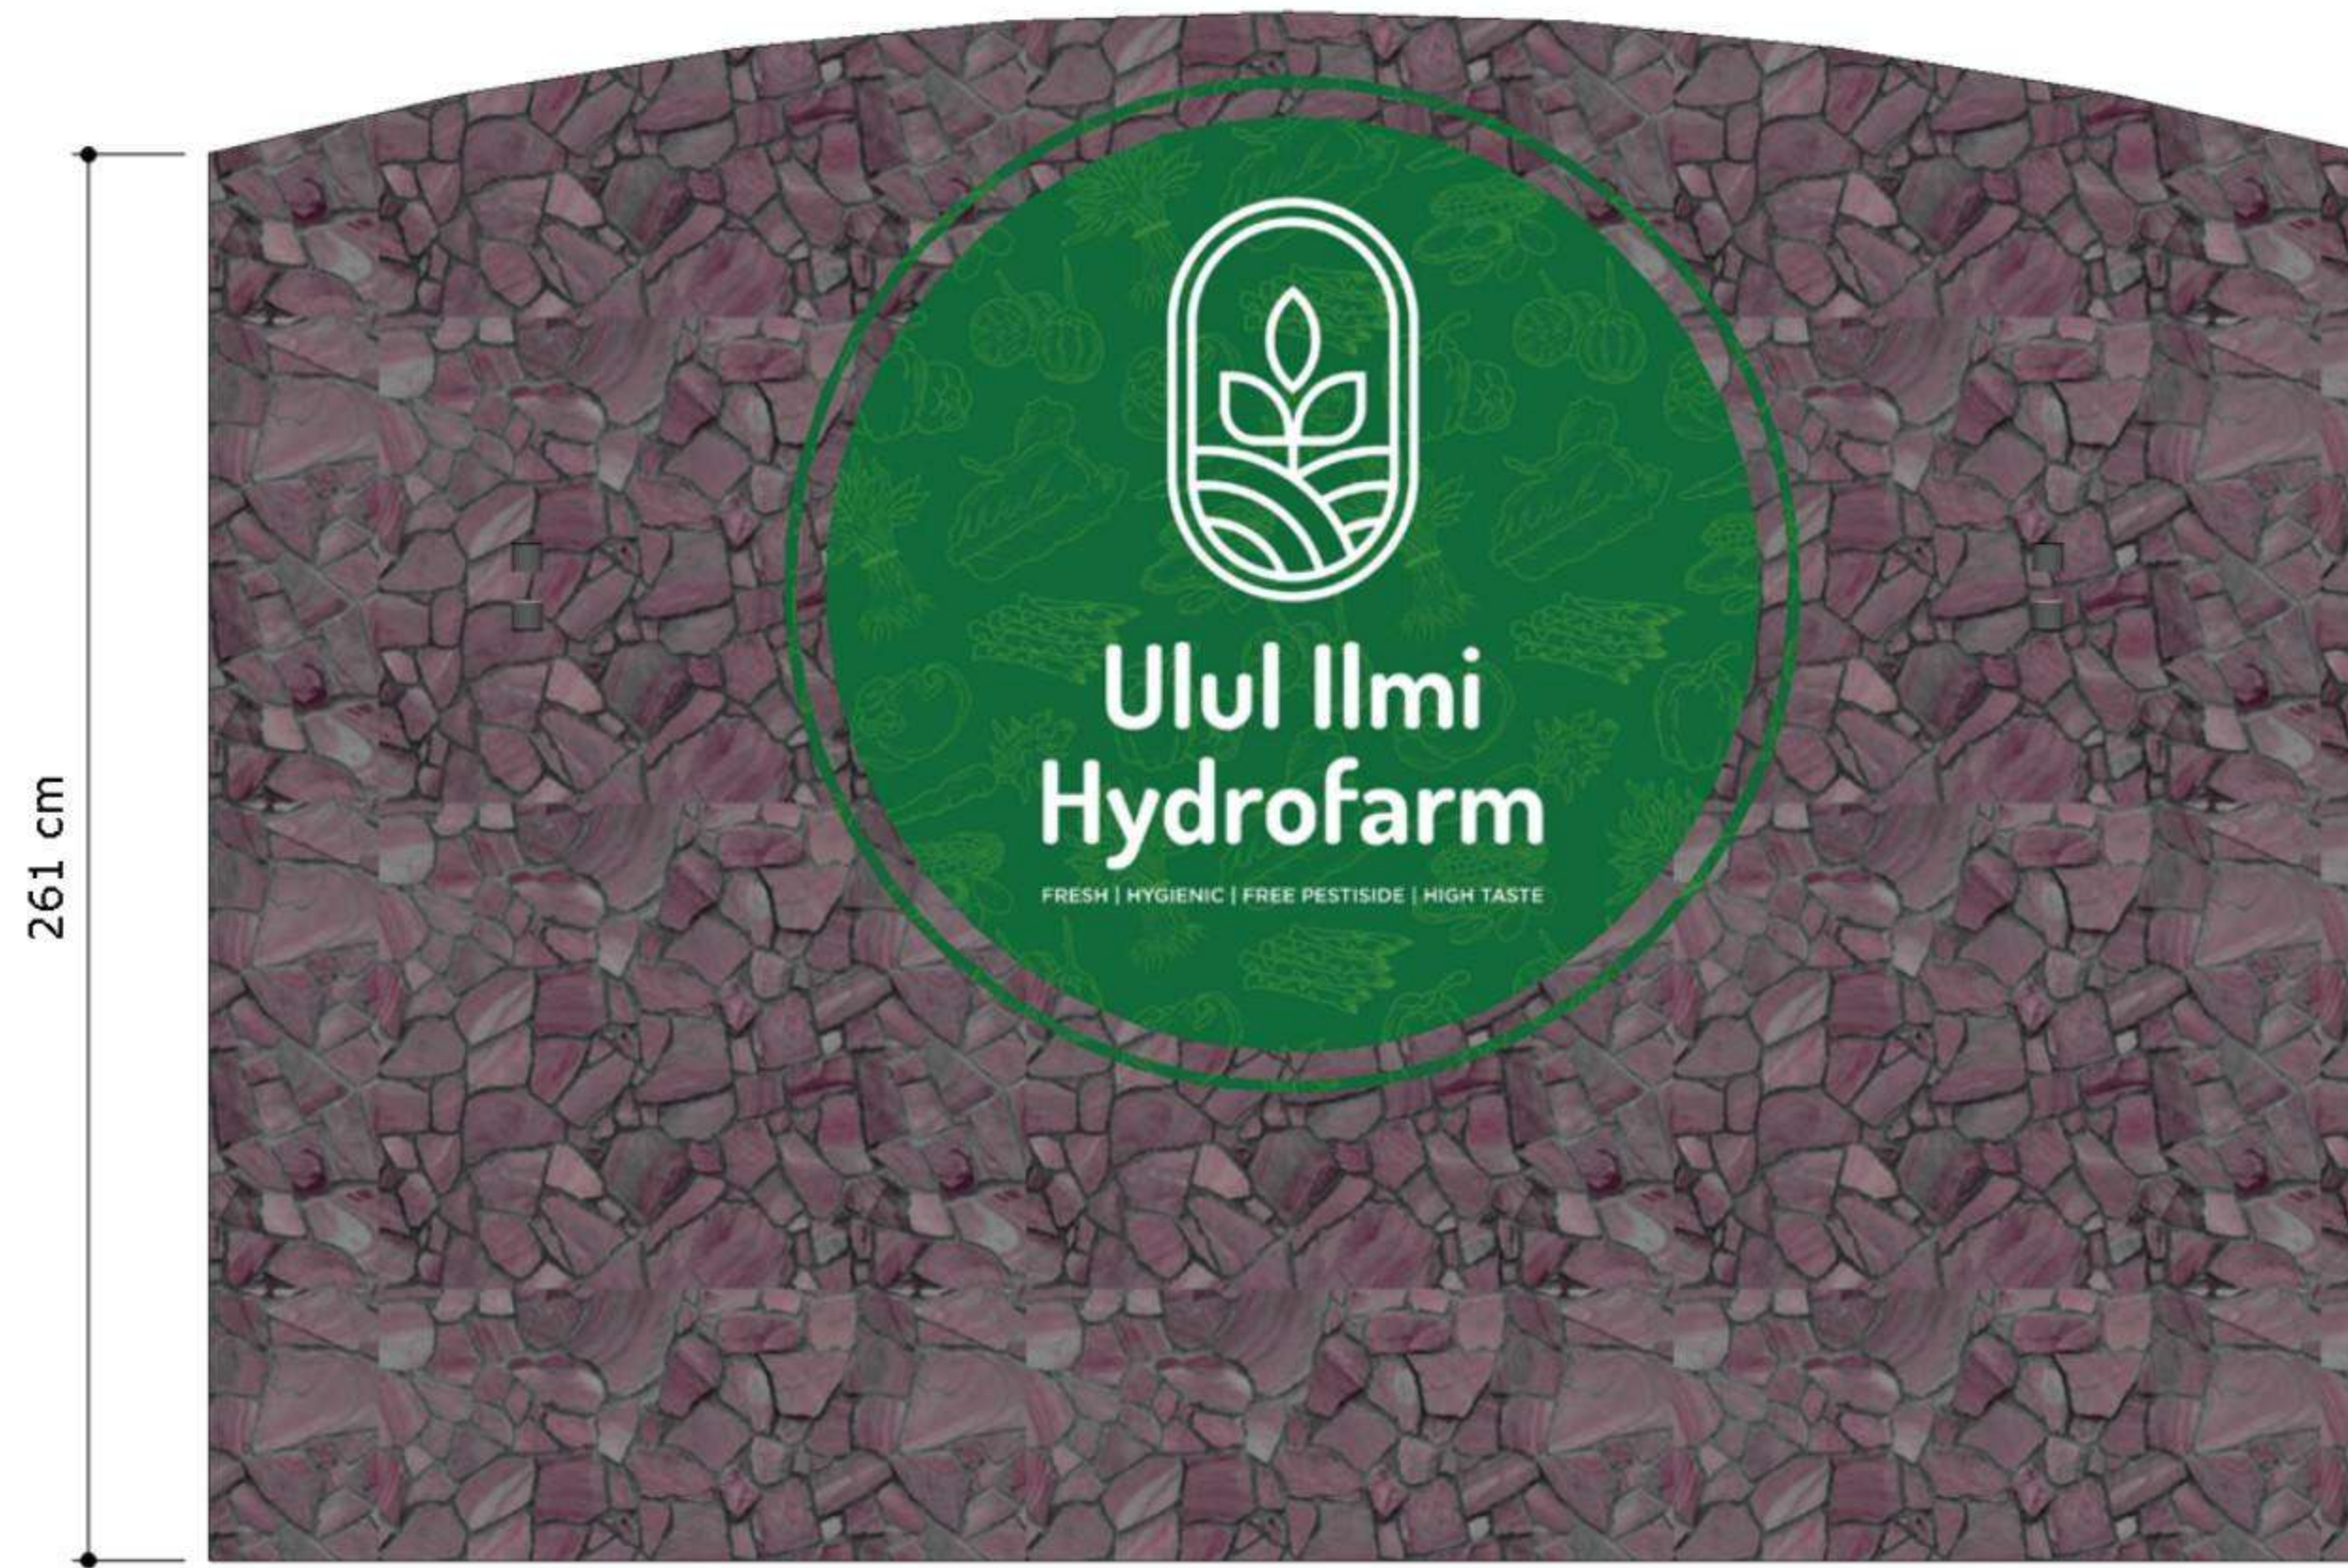

**TITLE WALL DETAIL**

1 : 15 SCALE



## PLANTER BOX DETAIL

1 : 15 SCALE



DAY PERSPECTIVE  
NTS



NIGHT PERSPECTIVE



Google

TRANSPSOED VIEW

NTS

